

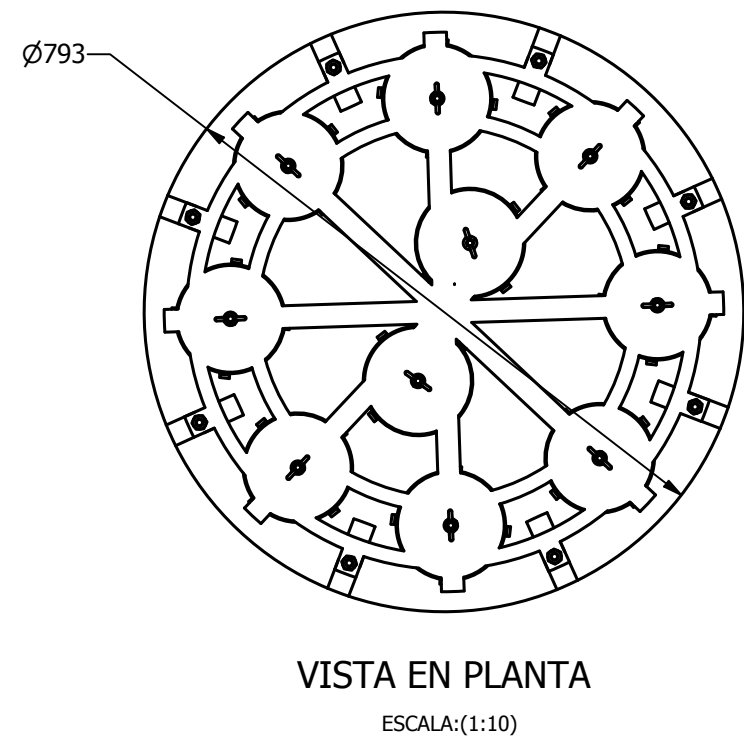
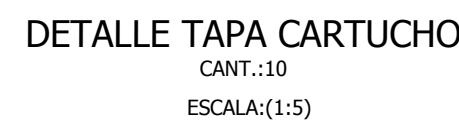
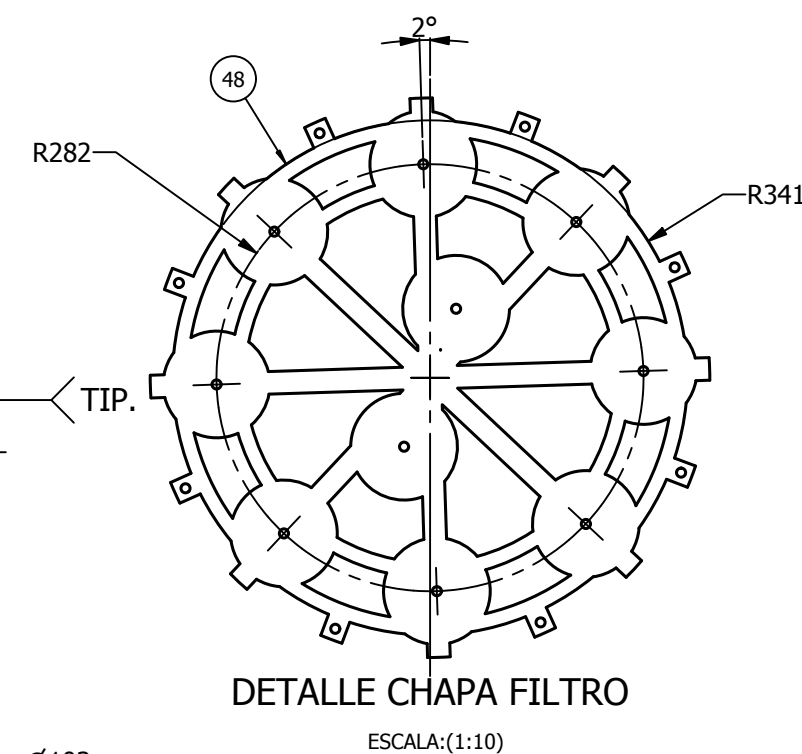
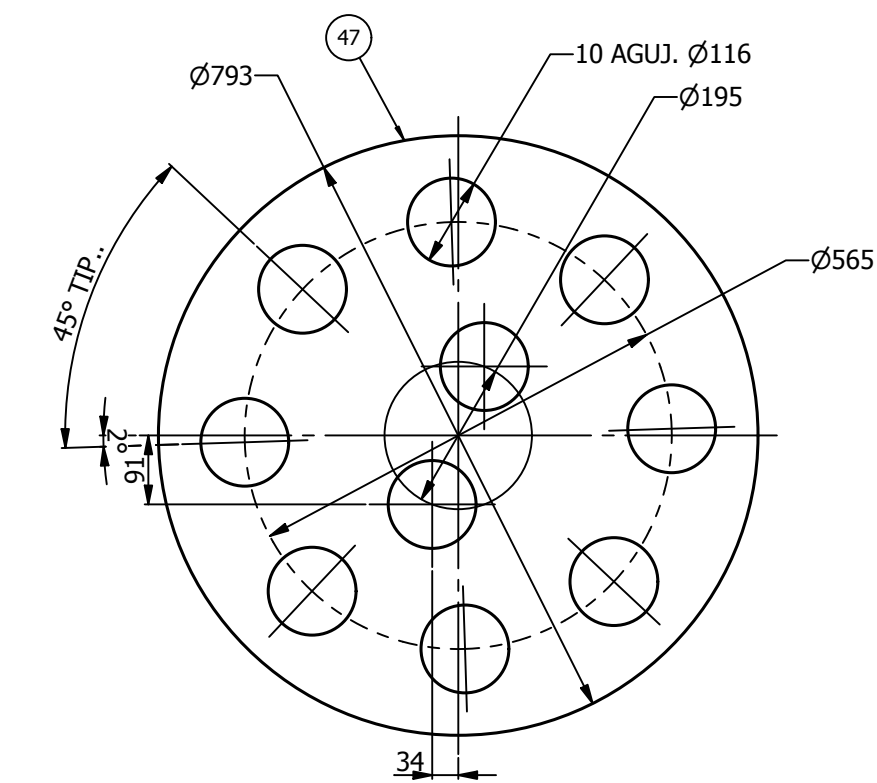
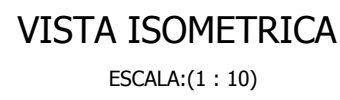



CANT.: 1

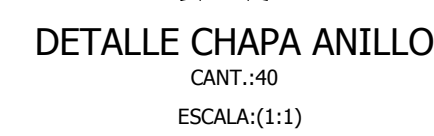

CANT.: 1

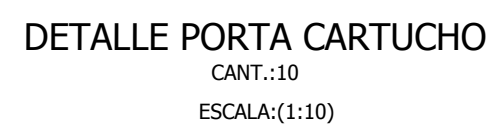


CANT.: 1

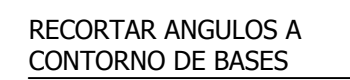


NOTA: AJUSTAR HOUSING CON CAJA DE CHICANAS

Las informaciones técnicas contenidas en este documento son propiedad exclusiva de "YPF" y por ende son confidenciales e intransferibles a terceros sin su previa autorización expresa. Asimismo, estos diagramas, así como los planos, se reservan todos los derechos de autor. No se permite la explotación económica ni la transformación de esta obra. Queda permitida la impresión en su totalidad o parcialmente para fines de información de carácter técnico, siempre y cuando se acredite el origen de la información de donde se obtuvo. No se permite la explotación económica ni la transformación de esta obra. Queda permitida la impresión en su totalidad o parcialmente para fines de información de carácter técnico, siempre y cuando se acredite el origen de la información de donde se obtuvo.	All technical information contained in this document is the exclusive property of "YPF" and may remain its confidential information without its prior written consent. Those drawings and diagrams are the property of YPF and are not to be reproduced, distributed or used in any form without its prior written consent.
---	--


CONEX. A

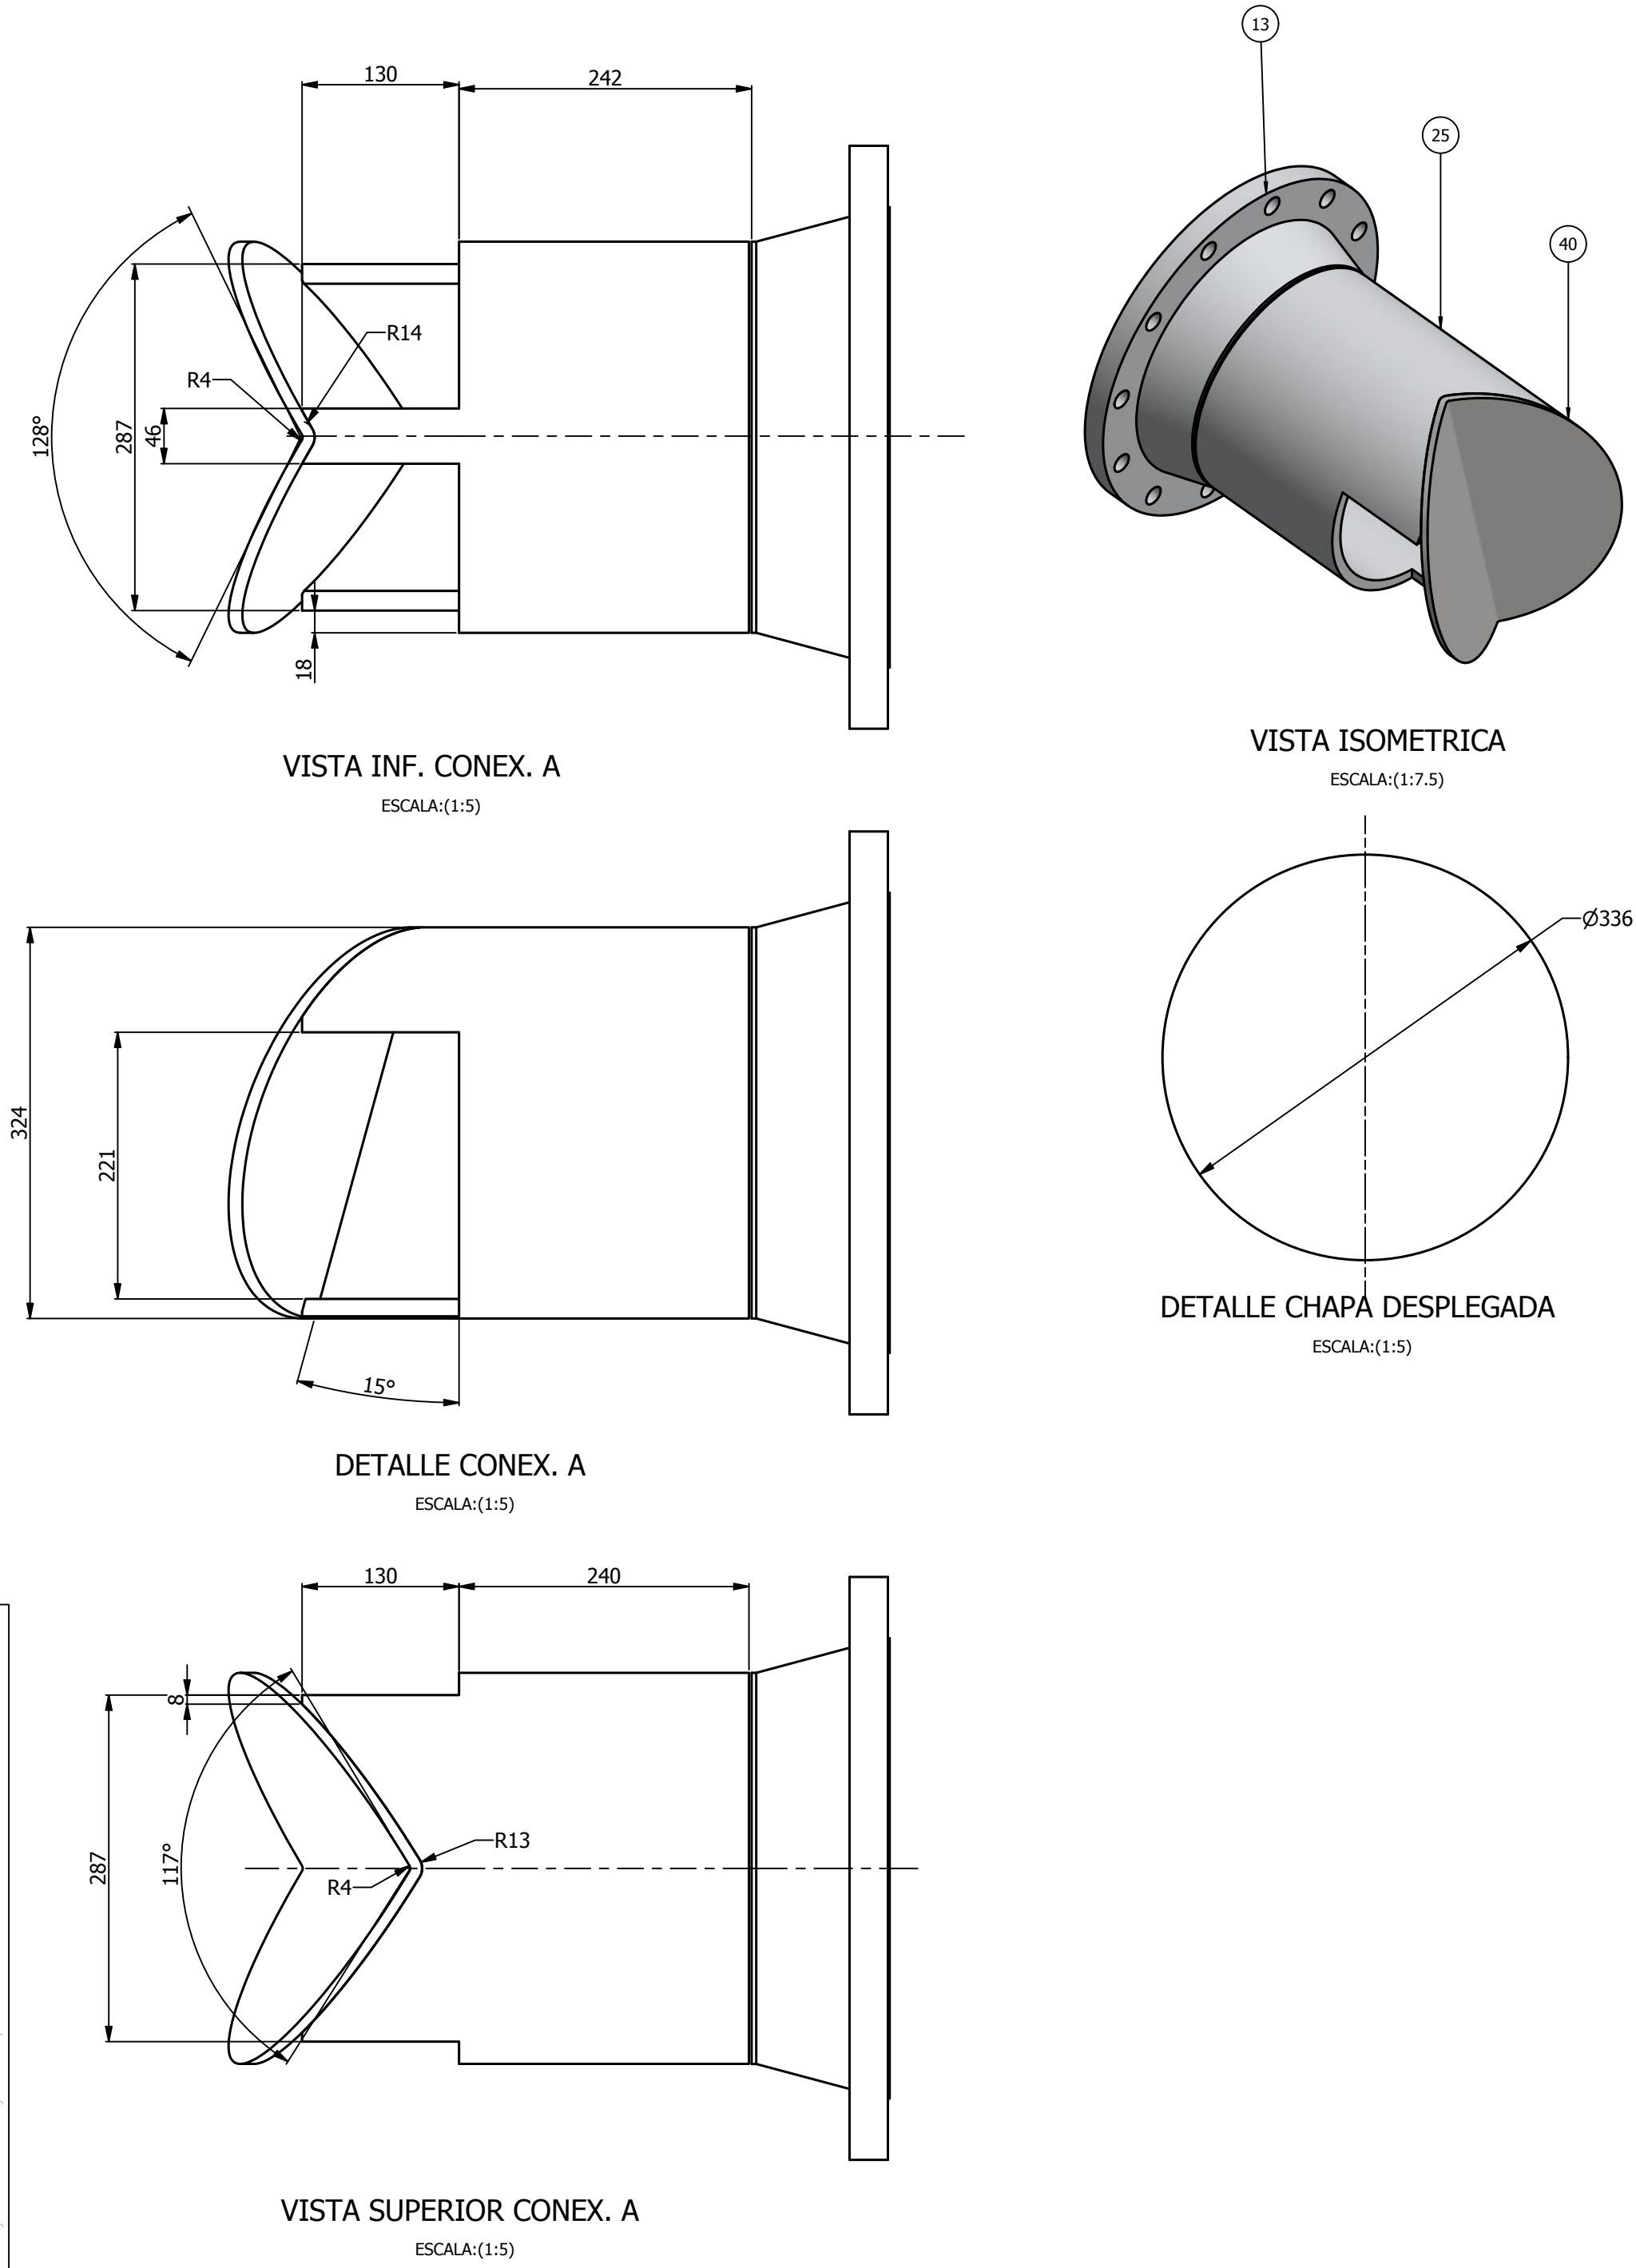


CARTELA

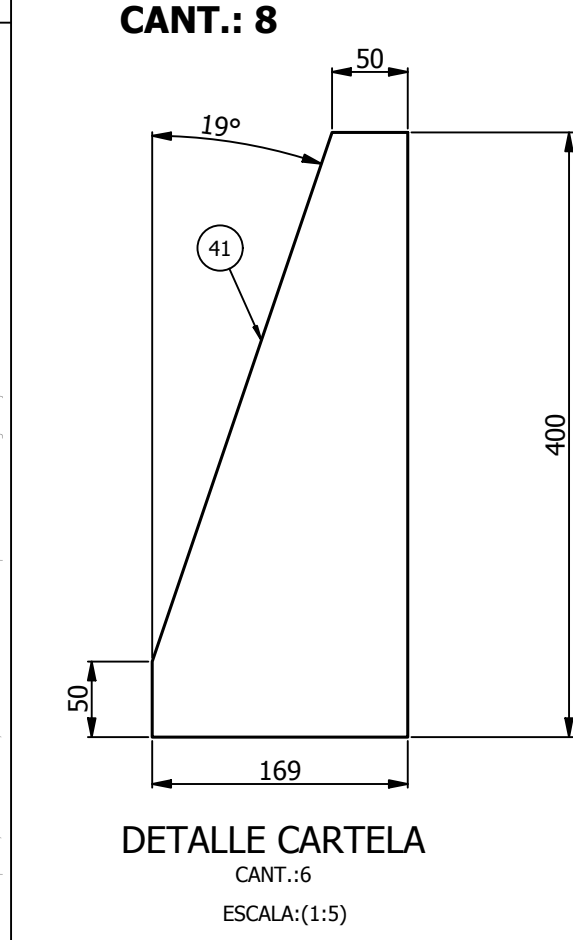


TAIL LUG

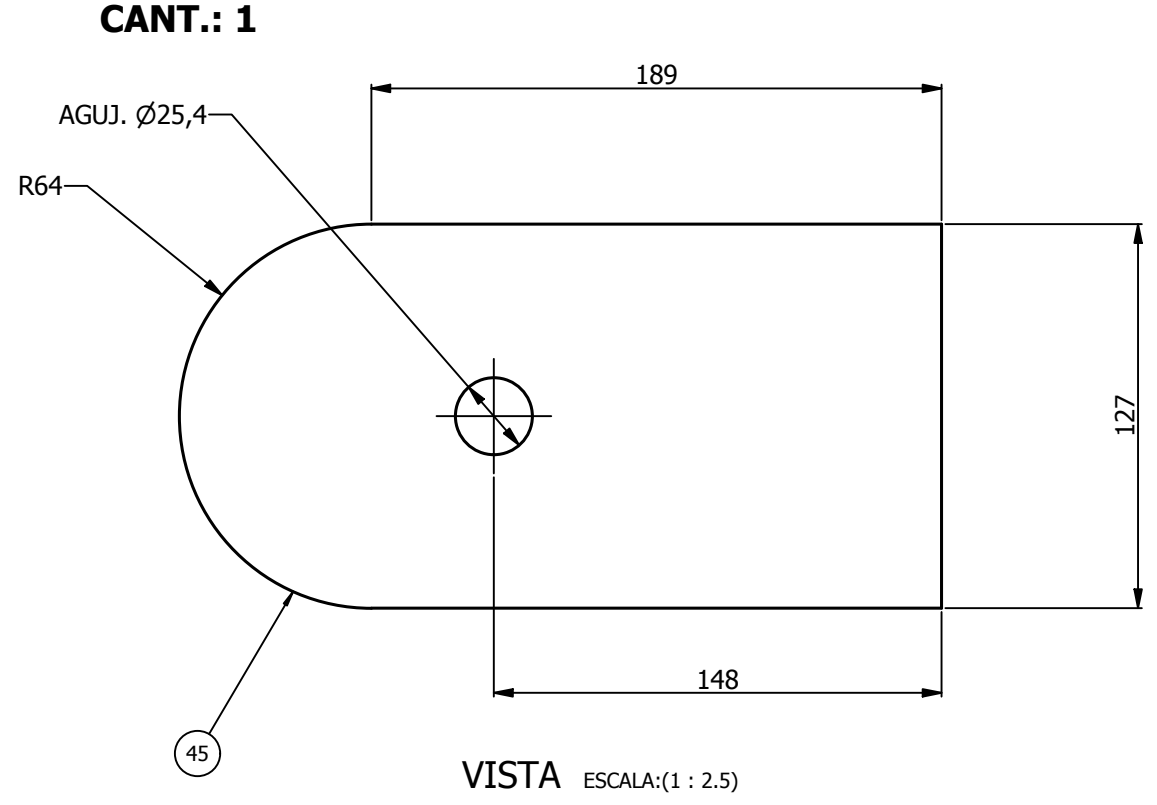


CANCAMO IZAJE

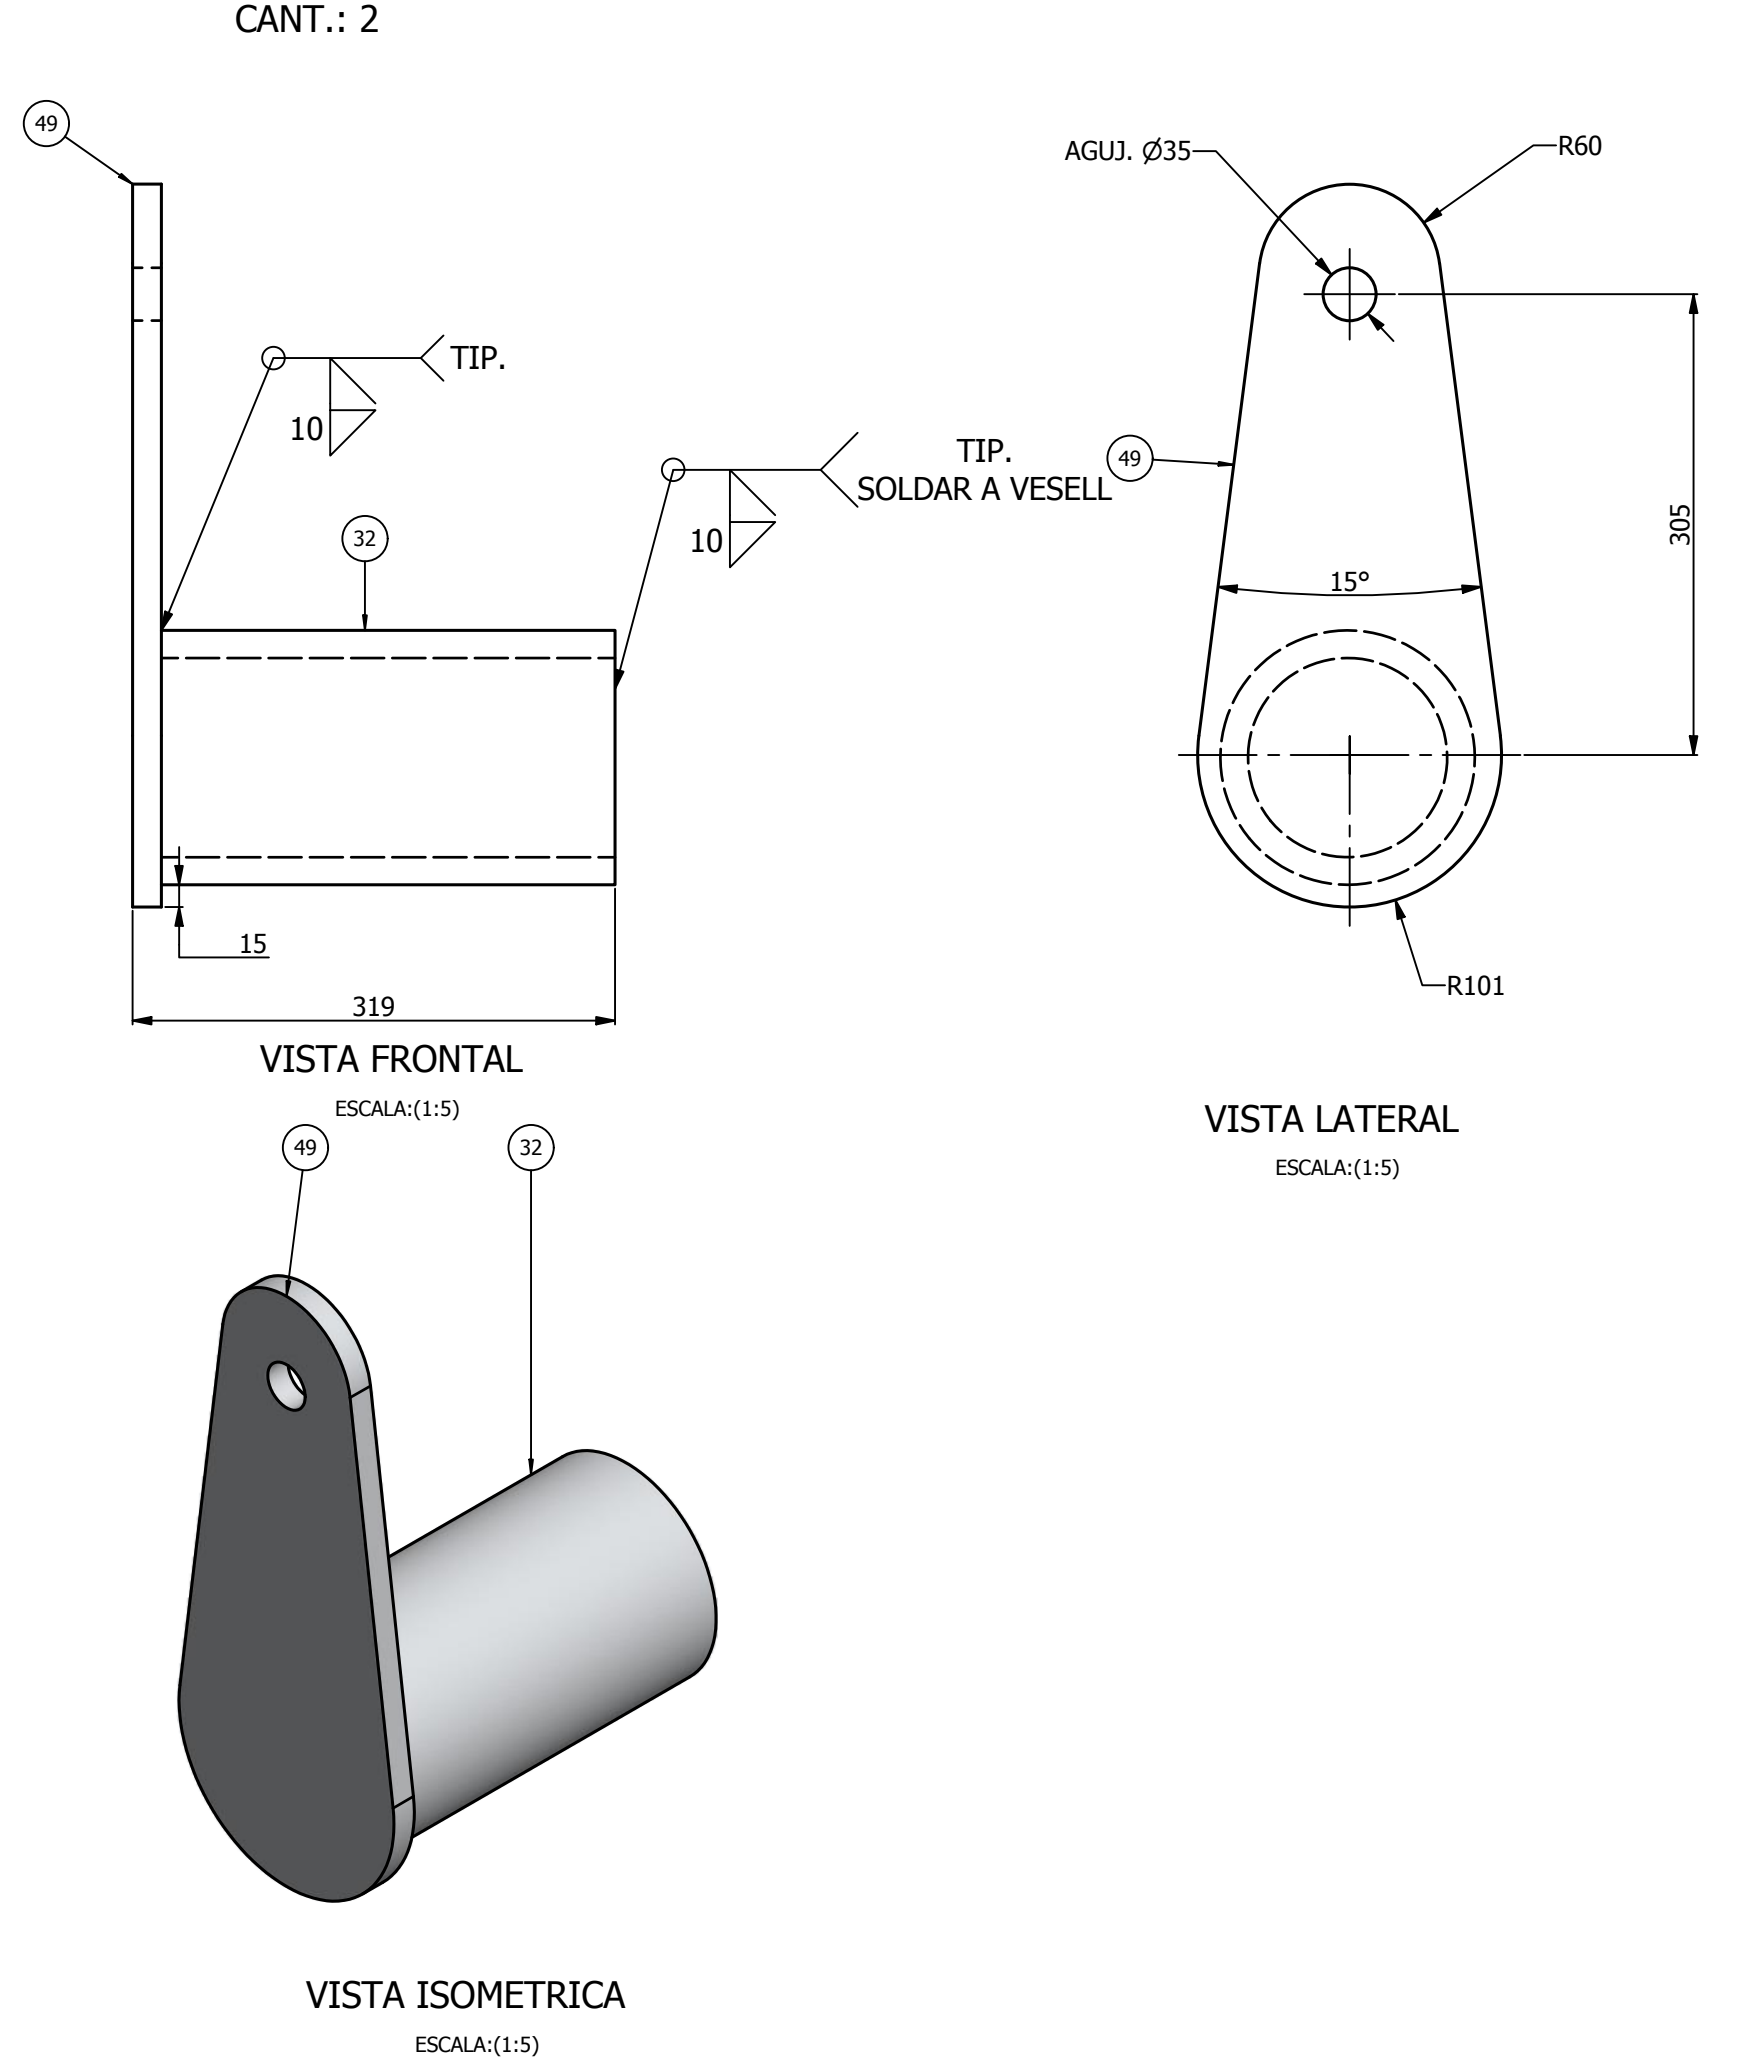

POLLERA

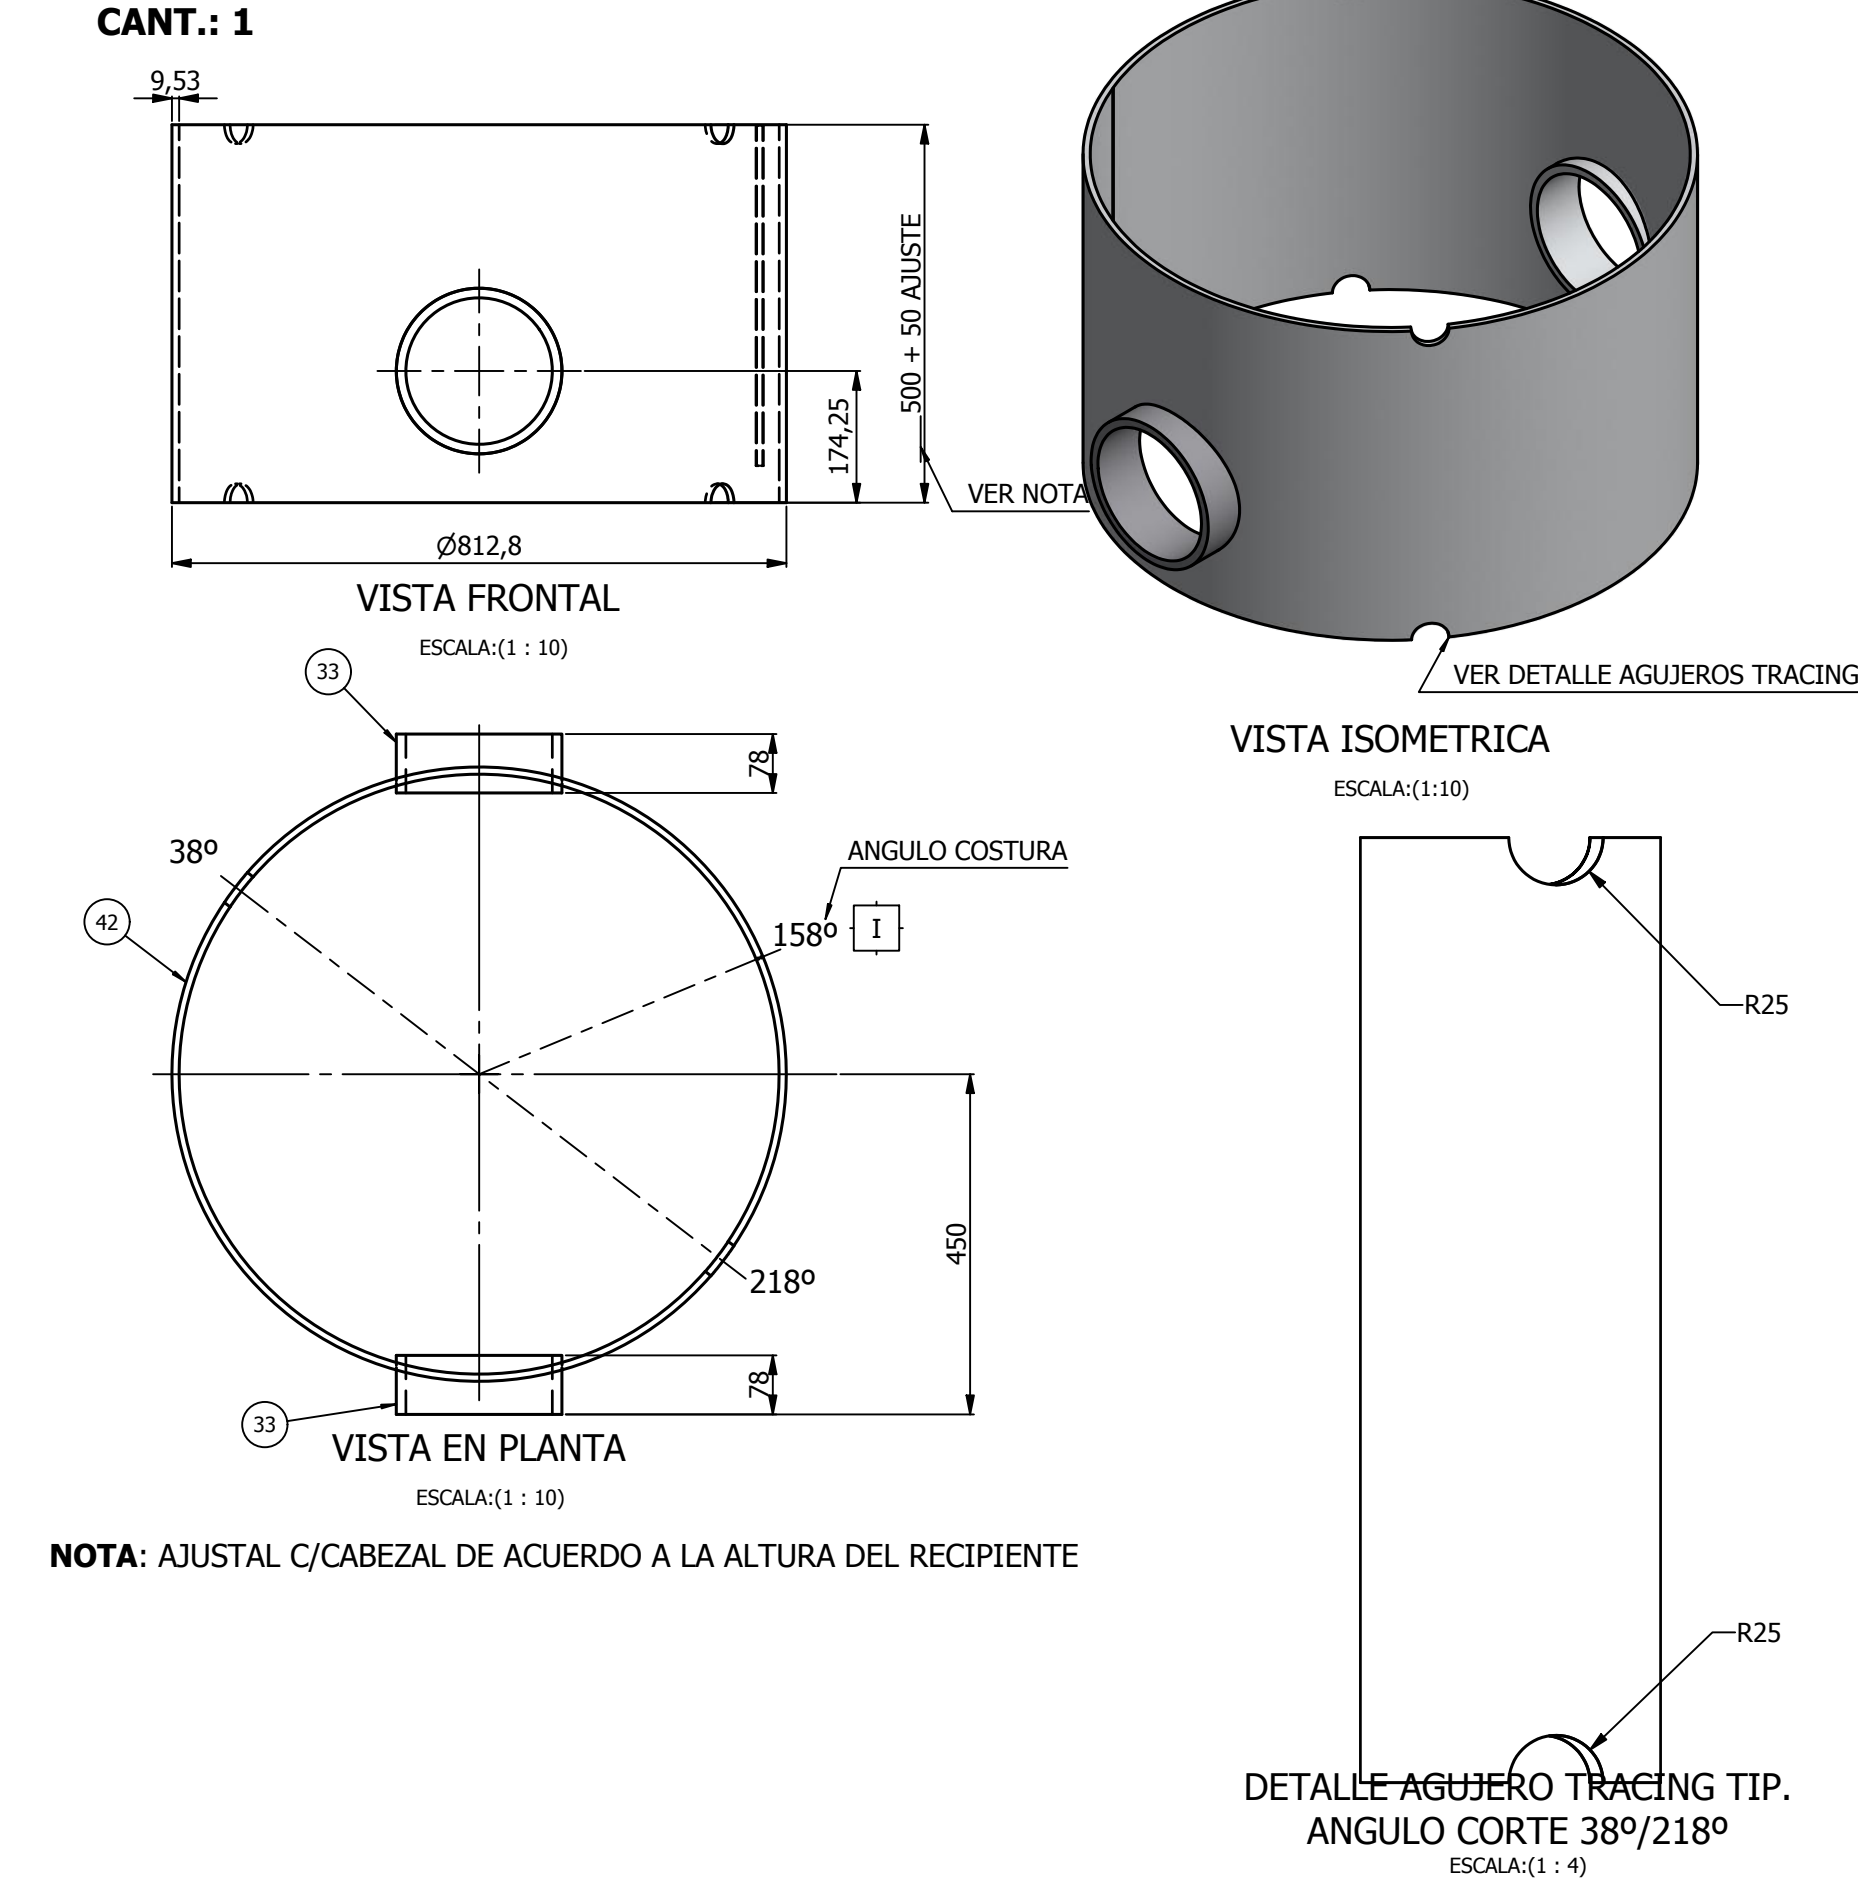


SOPORTE AISLACION

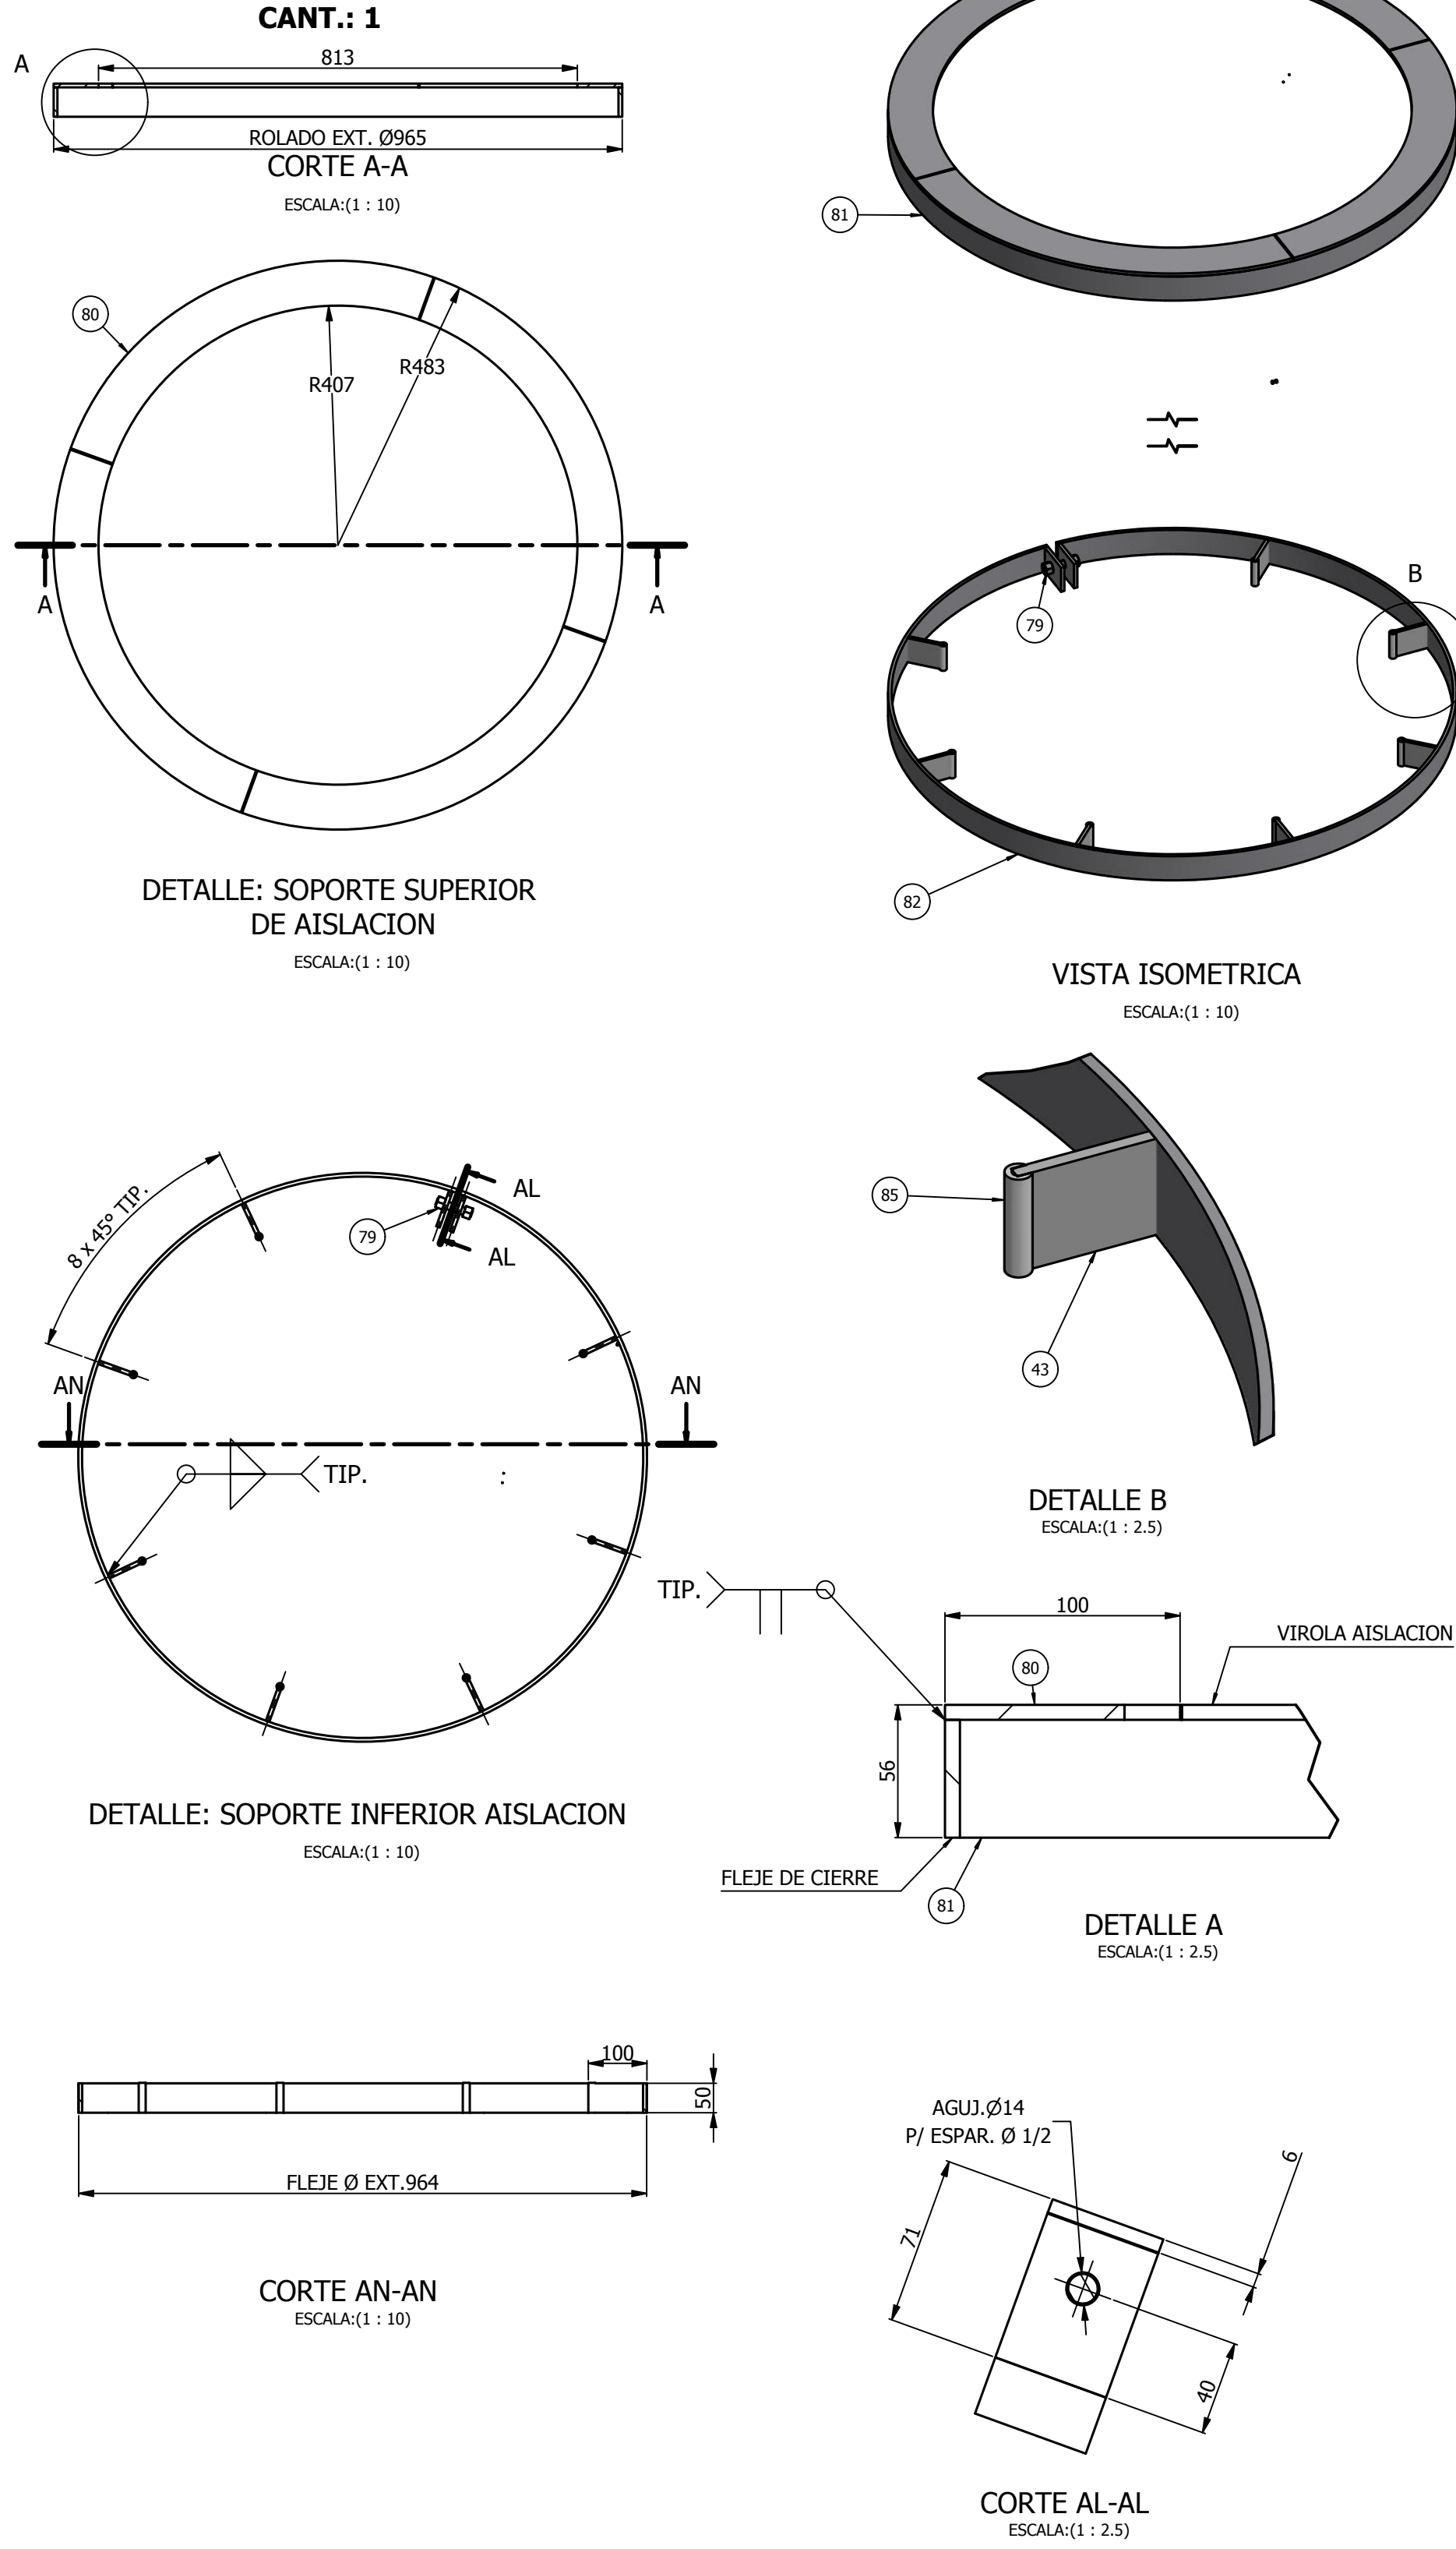


ROMPEVORTICES

CANT.: 1

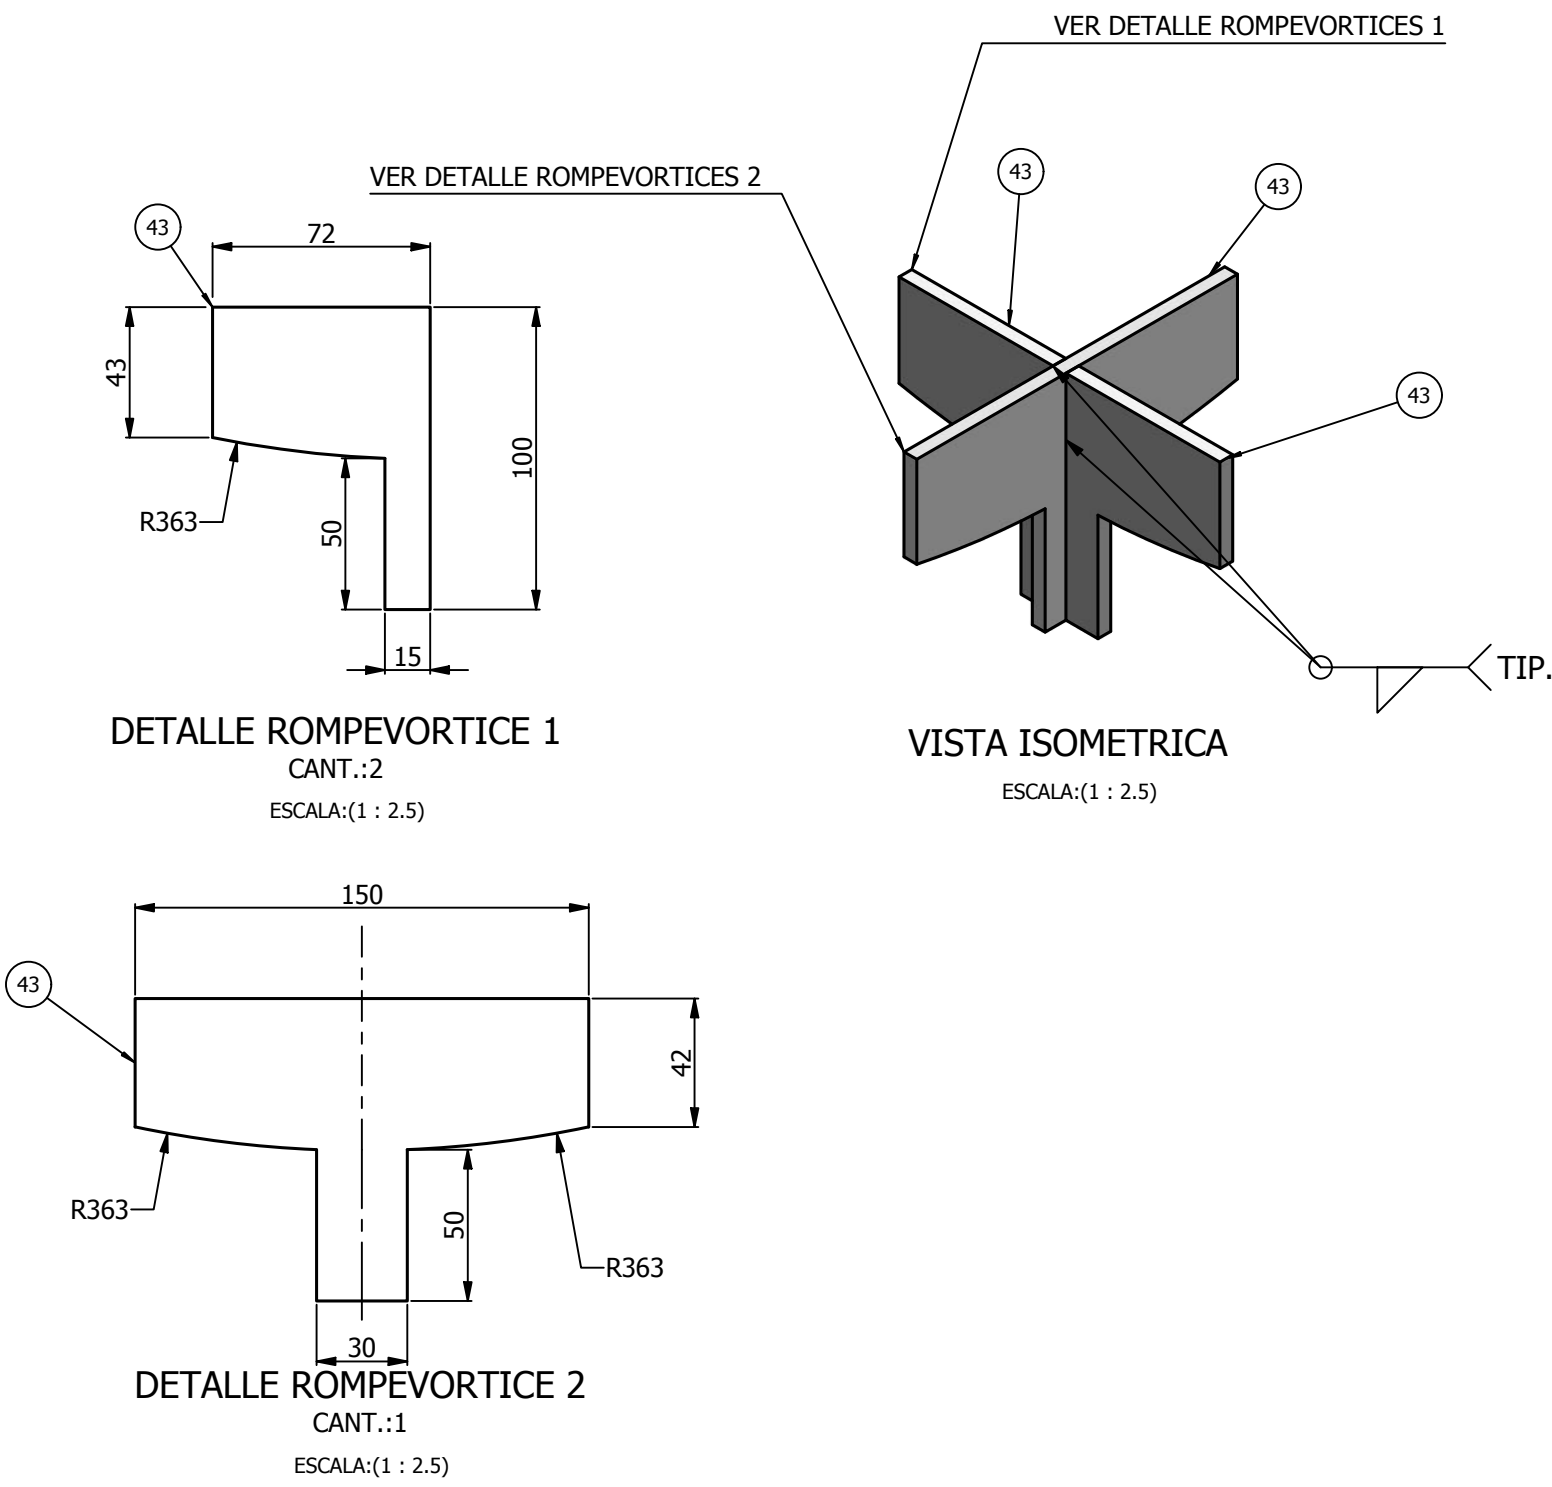


DETALLE MONTAJE ANODOS

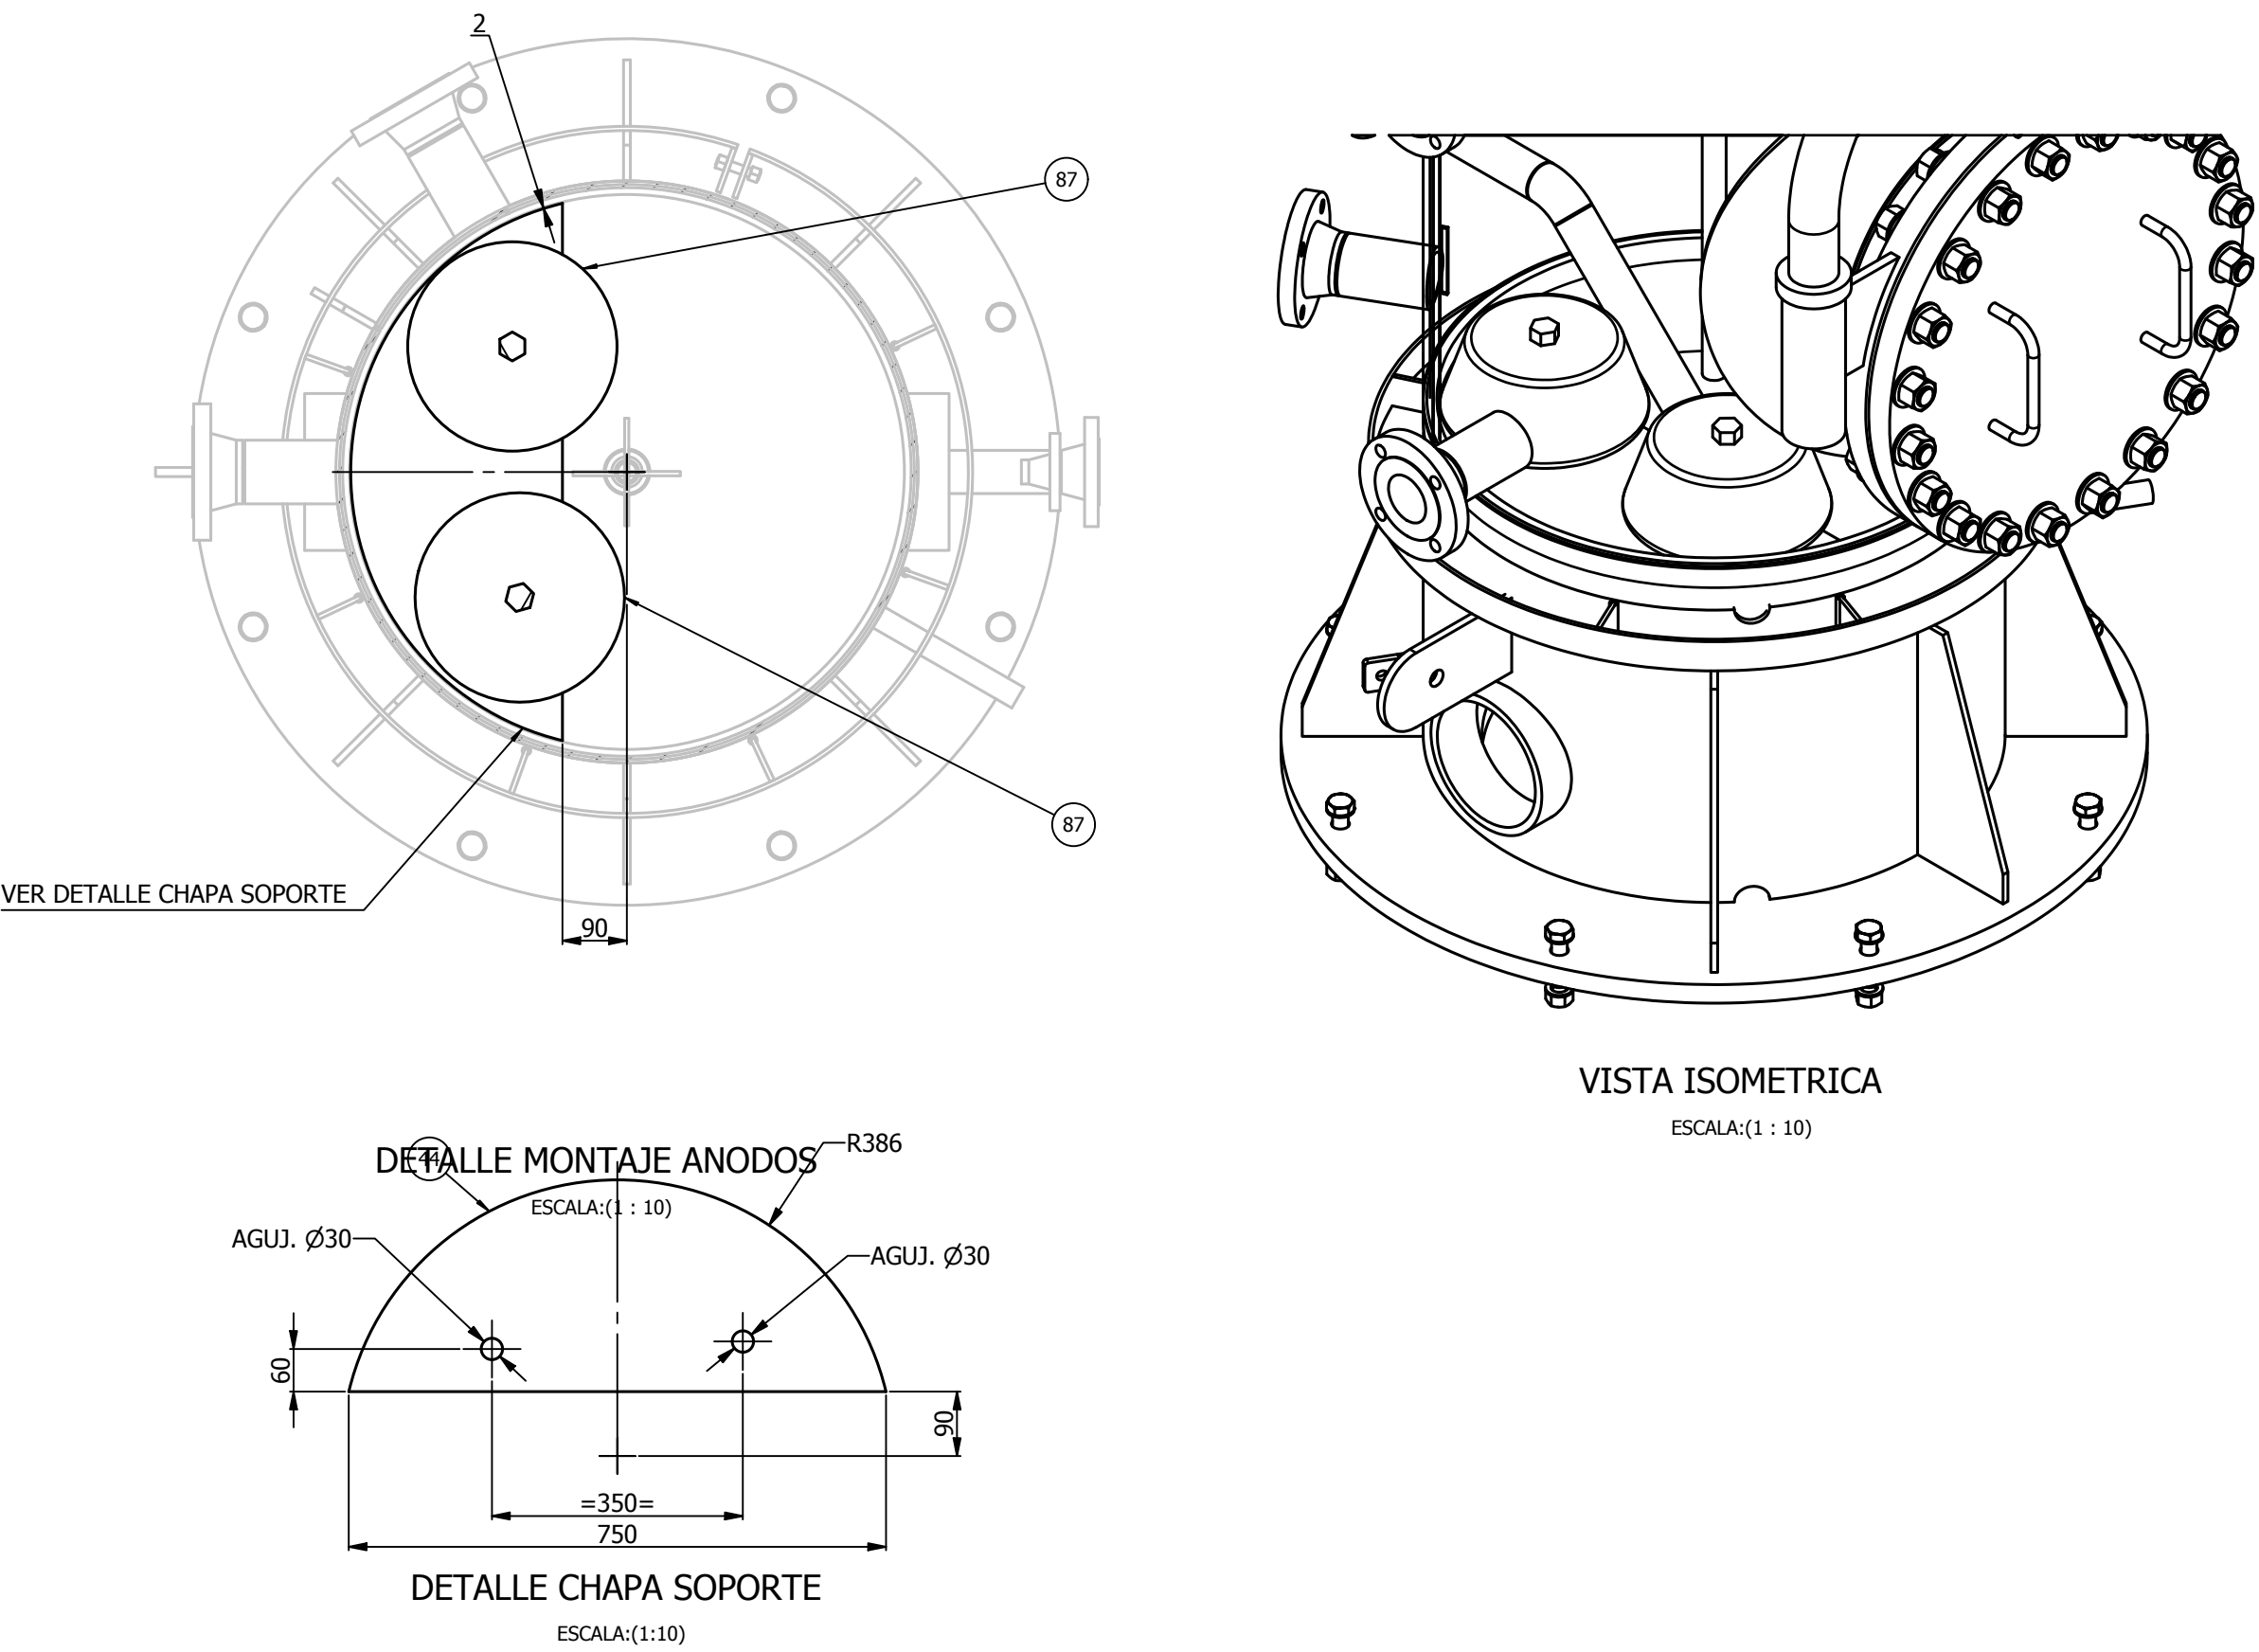


M2

CANT.: 1

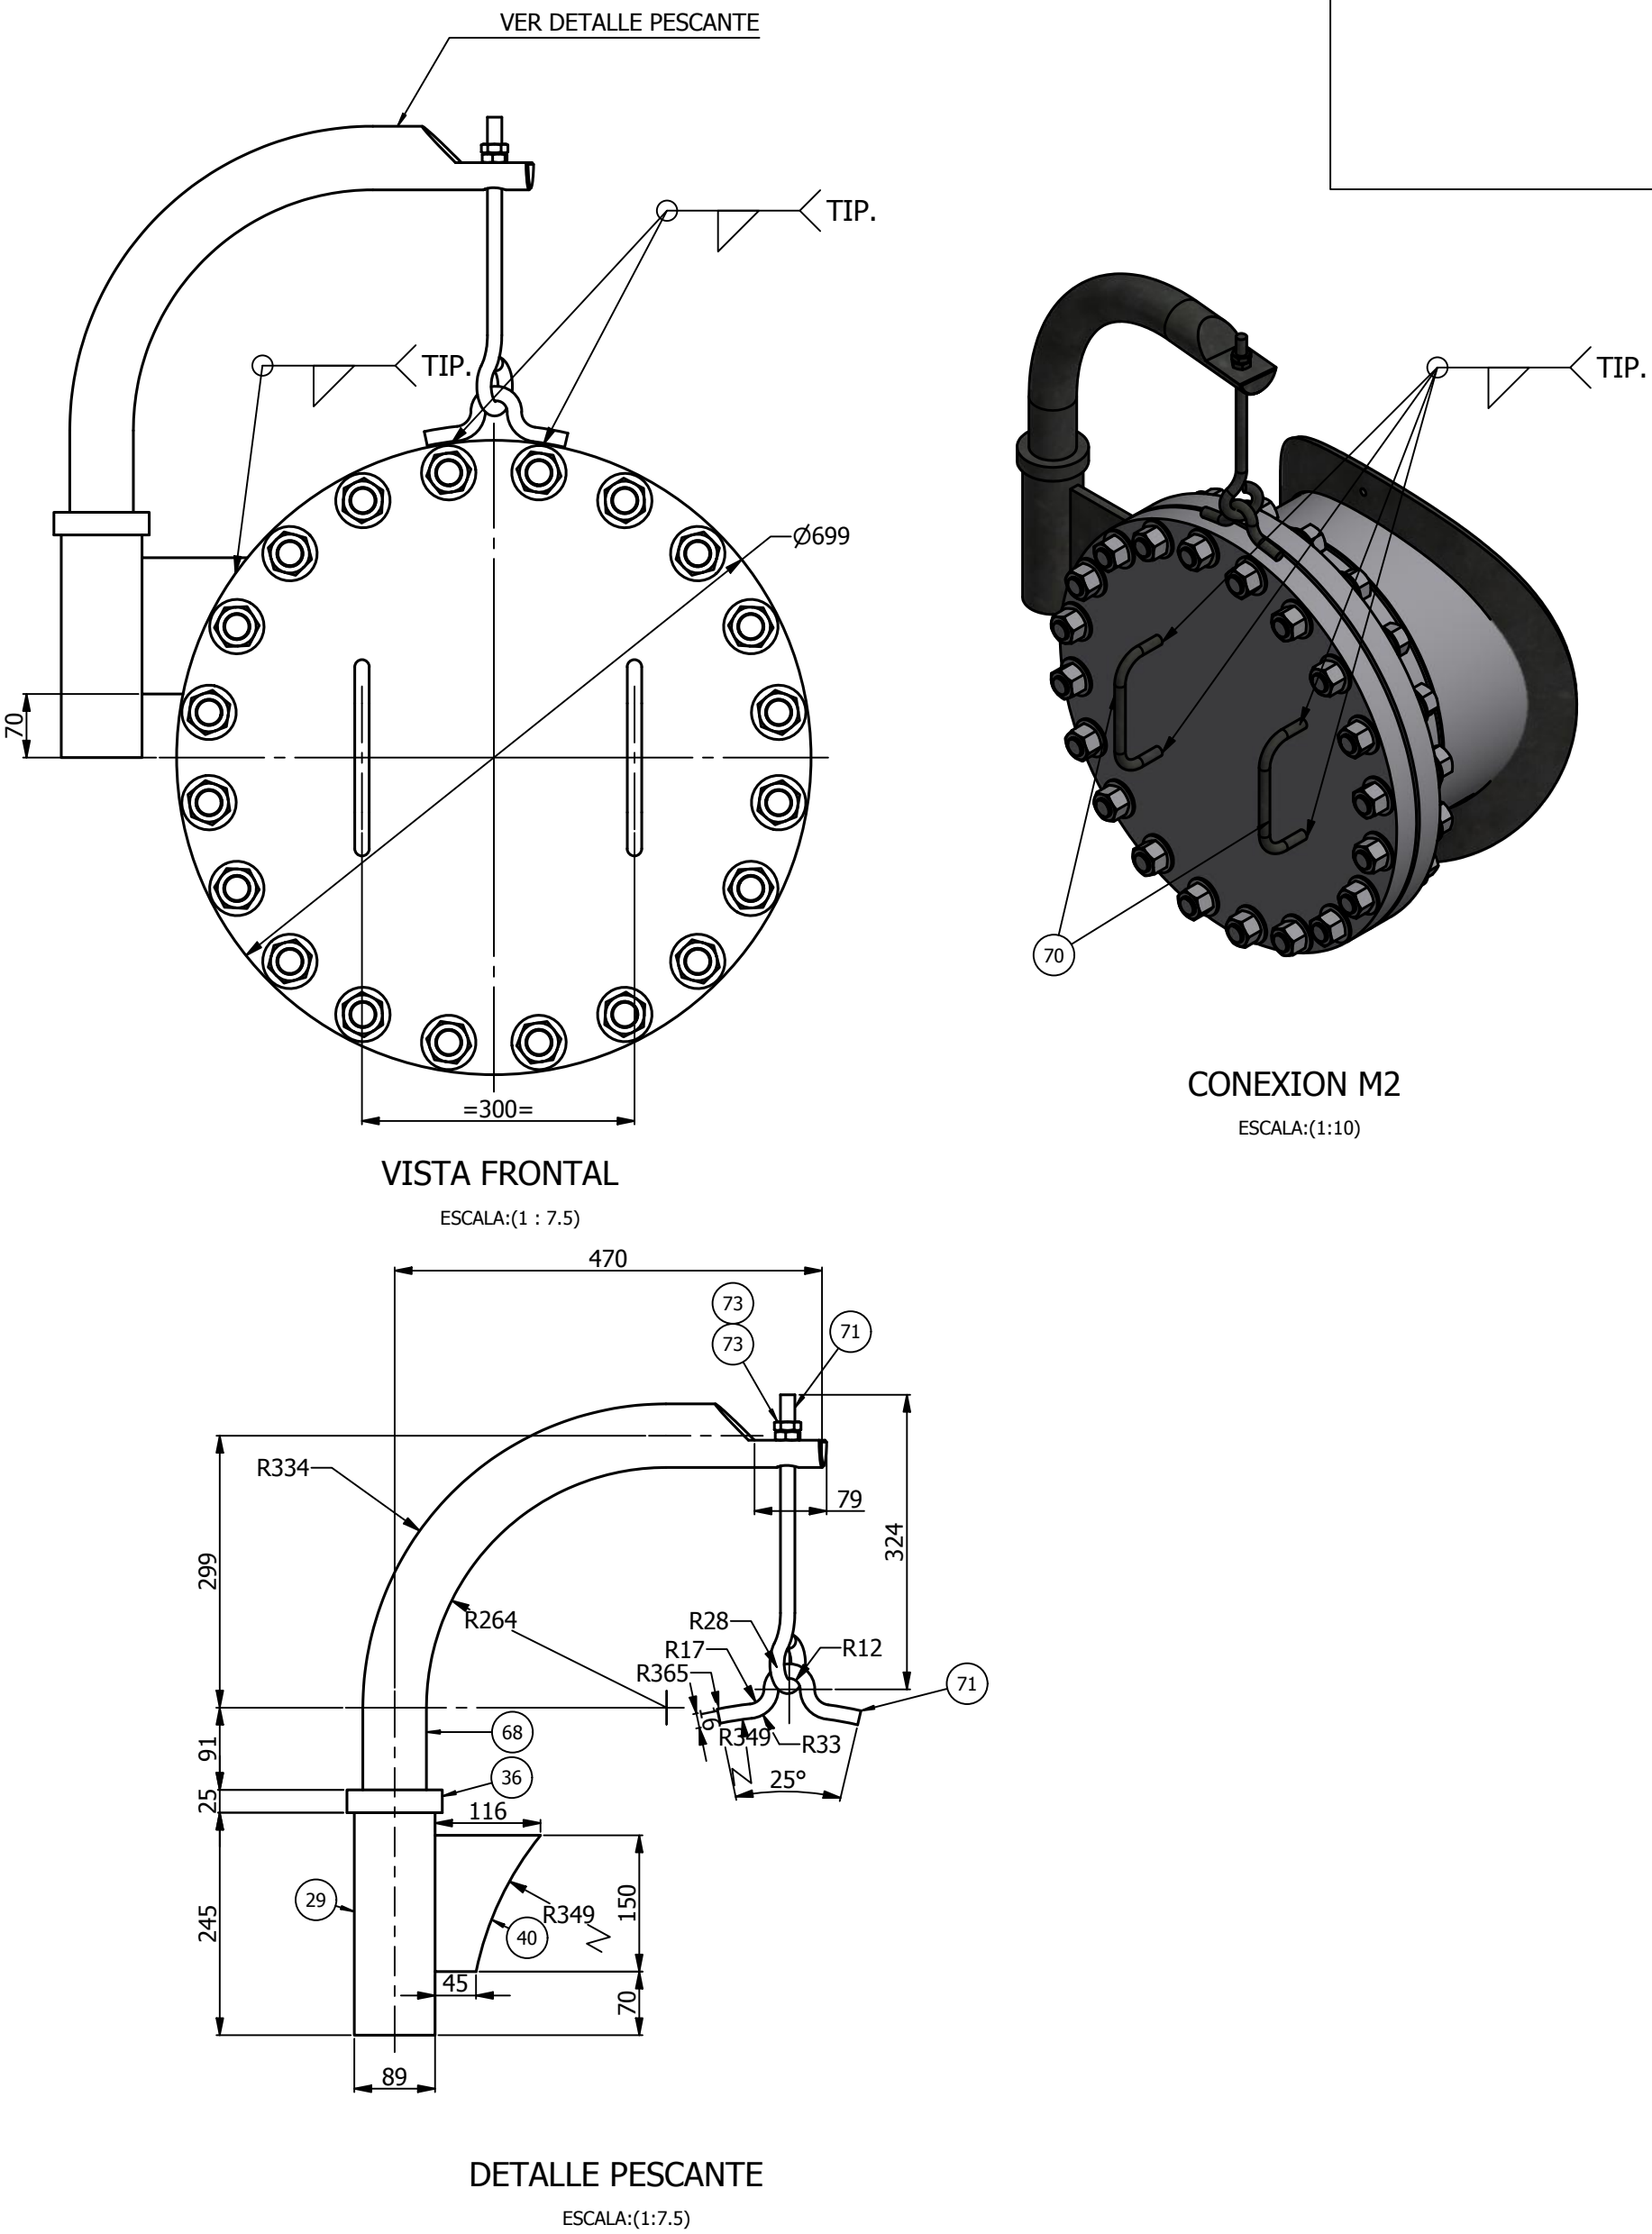

PESCANTE SUPERIOR

CANT.: 1

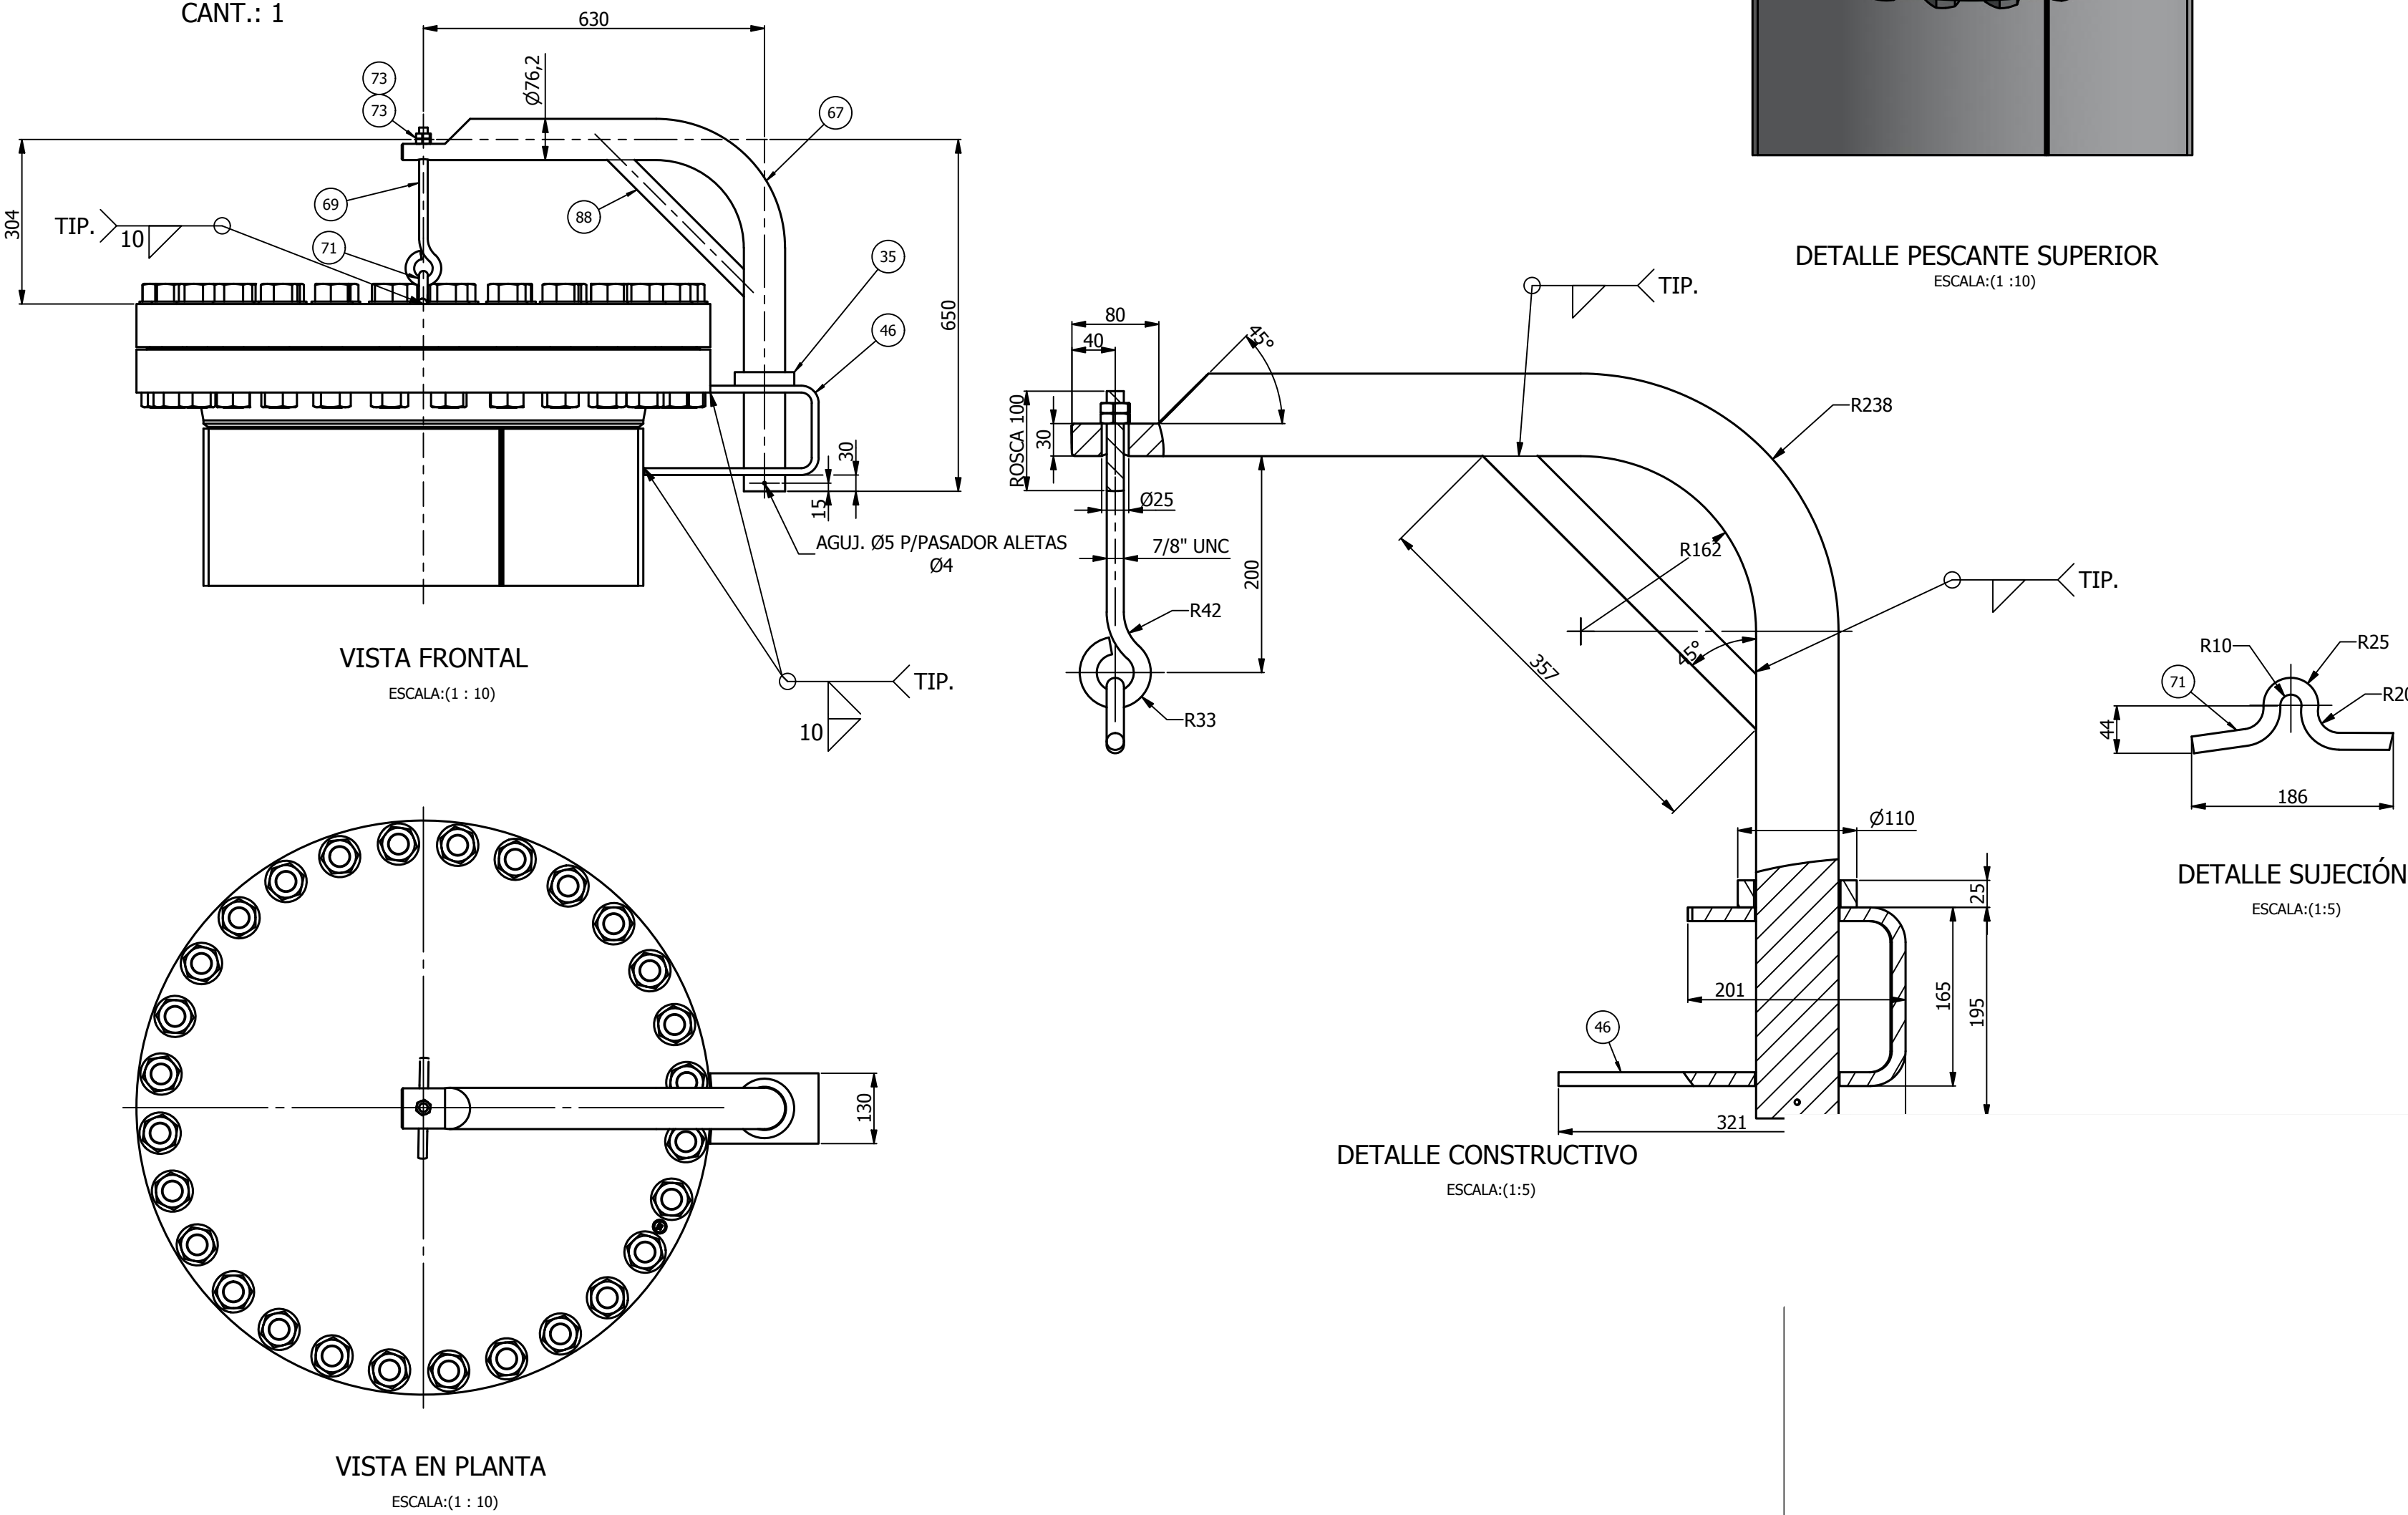

Los planos de este proyecto son propiedad de la empresa que los elaboró y no deben ser utilizados sin su expresa autorización escrita. Se prohíbe la reproducción, el uso no autorizado o la modificación de los planos sin el consentimiento escrito de la empresa que los elaboró. Los planos son válidos en su totalidad y no se aceptan modificaciones sin el consentimiento escrito de la empresa que los elaboró. Los planos son válidos en su totalidad y no se aceptan modificaciones sin el consentimiento escrito de la empresa que los elaboró.

4

3

2

1

DOCUMENTOS DE REFERENCIA:

- MBeC-CGEBER01-VCD16197-I-LY-049014- LAY OUT - CANALIZACIONES E INSTRUMENTOS FILTRO COALESCENTE
- MBeC-CGEBER01-VCD16197-R-PI-049023 - DIAGRAMA DE PROCESOS
- MBeC-CGEBER01-VCD16197-M-PL-049019-PLANO CONSTRUCTIVO VESSEL
- MBeC-CGEBER01-VCD16197-M-PL-049018-PLANO PIPING
- MBeC-CGEBER01-VCD16197-M-PL-049022-PLANO SKID, SOPORTES Y PLATAFORMAS
- MBeC-CGEBER01-VCD16197-M-PL-049021-PLANO PLACA IDENTIFICATORIA
- MBeC-CGEBER01-VCD16197-I-TI-049015- TIPICO MONTAJE DE INSTRUMENTOS FILTRO COALESCENTE

88	CHAPA ½" SA-516-70 100KG/M2	1		10001054
87	ANODO DE SACRIFICIO Ø 300 MM X 125 MM	2		50025331
86	REMACHE POP DE ALUMINIO Ø3.5x6mm	10 su		50016911
85	MANGUERA CRISTAL 6 MM	0,356 m		50000594
84	LANA MINERAL E=3" CON TEJIDO	3,500 m^2		50020854
83	CHAPA 0,80 mm ALUMINIO 2.2KG_M2	3,500 m^2		10002343
82	PLANCHUELA 2 x ¼ 2.53Kg_m	0,003 m		10000025
81	PLANCHUELA 2 x ¼ 2.53Kg_m	3,033 m		10000025
80	CHAPA ¼" SA-516-70 50KG/M2	0,000 m^2		10002340
79	ESPAR C/TUE Ø½X2½ UNC SA-193-B7 BIC	1		50030947
78	VARILLA ROSC BSW Ø3_8X1M SAE 1010	10		50001112
77	TUERCA MAR BSW 3_8 AC GALV	10		50018353
76	TUERCA HEX UNC 7_8 DIN934 AC	8		50004256
75	TUERCA HEX UNC 3/8" DIN934 SA-194-2H BIC	8		50004606
74	TUERCA HEX UN 1½" DIN934 SA-194-2H BICR	56		50005413
73	TUERCA HEX BSW ¾" DIN934 BICR	4		50025640
72	SOPORTE PLACA IDENTIFICATORIA	1	PL. COM-G0006-M-PR-14389	
71	REDONDO Ø7/8" SAE1010/20 3.04KG/M	1,807 m	*Varía*	10000067
70	REDONDO Ø5/8" SAE1010/20 1.55KG/M	0,720 m		10000072
69	REDONDO Ø5/8" SAE1010/20 1.55KG/M	0,260 m		10000072
68	REDONDO Ø2¾" SAE1010/20 30KG/M	1,135 m		10000068
67	REDONDO Ø3" SAE1010/20 35.77KG/M	1,320 m		10000520
66	PLANCHUELA COBRE ELECTROLITICO 50X10MM	2		10000901
65	PLANCHUELA 2" X 3/8" 3.80KG/M	0,100 m		10000031
64	PLANCHUELA 1" X ¼" 1.28KG/M	1,458 m		10000922
63	MED CUPLA NPS ½ CL6000 NPT SA105	4		50006911
62	MED CUPLA NPS 1" CL3000 NPT SA105	1		50006150
61	JUNTA ESP. A-I-C NPS 4" CL150 AISI316	2		50009889
60	JUNTA ESP. A-I-C NPS 32" CL150 AISI316	1		50047270
59	JUNTA ESP. A-I-C NPS 20" CL150 AISI316	1		50006120
58	JUNTA ESP. A-I-C NPS 2" CL150 AISI316	4		50009891
57	ESPAR Ø1½ X 9 UN SA-193-B7 BICR	28	TORQUE:320 kgm:2314.6 lb.pie	50012224
56	ESPAR C/TUE Ø5/8"X4" UNC SA-193-B7 BIC	16		50023480
55	ESPAR C/TUE Ø5/8"X3¾" UNC SA-193-B7 BIC	16		50006909
54	ESPAR C/TUE Ø1 1/8 X 6¾ UN SA-193-B7 BIC	20		50027944
53	ELEMENTO FILTRANTE GORA MOD. 54305	10		50047211
52	CUPLA NPS ½ CL3000 NPT SA105	10		50009902
51	CODO 90º RL NPS 2" SCH160 BW SA234WPB	1		50008502
50	CODO 45º RL NPS 2 SCH160 BW SA234WPB	1		50013729
49	CHAPA ¾" SA-516-70 150,7KG/M2	0,180 m^2		10001400
48	CHAPA ½" SA-516-70 100KG/M2	1,350 m^2		10001054
47	CHAPA ½" SA-516-70 100KG/M2	1,350 m^2		10001054
46	CHAPA ½" SA-516-70 100KG/M2	0,000 m^2		10001054
45	CHAPA ½" IRAM F24 100,5KG/M2	0,019 m^2		10000713
44	CHAPA ½ SA-516-70 100KG_M2	0,170 m^2		10001054
43	CHAPA ¼" SA-516-70 50KG/M2	2,522 m^2		10002340
42	CHAPA 3/8" SA-516-70 75KG/M2	11,850 m^2		10001415
41	CHAPA 3/8" SA-516-70 75KG/M2	0,541 m^2		10001415
40	CHAPA 3/8" SA-516-70 75KG/M2	0,197 m^2		10001415
ITEM	DESCRIPCION	CANT.	OBSERVACION	SAP
LISTA DEMATERIALES				

39	CHAPA 3/16" IRAM F24 37,4 KG/M2	0,106 m^2		10002275
38	CHAPA 1¼" IRAM F26 251,2KG/M2	1,464 m^2		10000723
37	CHAPA 1,5 mm INOX AISI 304 12,0KG/M2	0,023 m^2		10002324
36	CHAPA 1" IRAM F26 200,9KG/M2	0,011 m^2		10002314
35	CHAPA 1" IRAM F26 200,9KG/M2	0,012 m^2		10002314
34	CAÑO S/C NPS ½ SCH80 SA 106 GR B	8,35 m		10004720
33	CAÑO S/C NPS 8 SCH40 SA 106 GR B	0,16 m		10001414
32	CAÑO S/C NPS 6 SCH160 SA 106 GR BV	0,60 m		10001148
31	CAÑO S/C NPS 4 SCH80 SA 106 GR B	0,30 m		10000689
30	CAÑO S/C NPS 4 SCH40 SA 106 GR B	5,00 m		10001408
29	CAÑO S/C NPS 3 XXS SA 106 GR B	0,25 m		10001151
28	CAÑO S/C NPS 3 SCH80 SA 106 GR B	3,00 m		10001565
27	CAÑO S/C NPS 20 SCH20 SA 106 GR B	0,20 m		10001555
26	CAÑO S/C NPS 2 SCH160 SA 106 GR B	2,73 m		10001413
25	CAÑO S/C NPS 12 SCH20 SA 106 GR B	0,67 m		10001540
24	CAÑO S/C NPS 1 SCH40 SA 106 GR B	1,00 m		10000676
23	CAÑO S/C NPS 1 SCH160 SA 106 GR B	1,30 m		10001342
22	CAJA CHICANA 800x650x203mm F.HOR-DB-316	1		50044861
21	CAB ELIP 2:1 Ø812,8MM ¾" SA516 GR70	1		50043470
20	BULON H UNC 7/8"x3¼" DIN931 SAE-8 BICR	8		50017198
19	BULON H UNC 3/8" X 1¼" DIN933 SAE-5 BICR	8		50010980
18	BRIDA WNRF NPS 4 CL150 SCH80 SA105	2		50008568
17	BRIDA WNRF NPS 32 #150 A ESP 3-8 SA105	1		50047182
16	BRIDA WNRF NPS 3 CL150 SCH80 SA105	10	TORQUE: 217 Nm 160 lb-ft	50006829
15	BRIDA WNRF NPS 20 CL150 SCH 20 SA-105	1		50026270
14	BRIDA WNRF NPS 2 CL150 SCH160 SA105	8		50009757
13	BRIDA WNRF NPS 12 CL150 SCH20 SA105	2		50007812
12	BRIDA WNRF NPS 1"CL150 SCH160 SA105	4		50005957
11	BRIDA BLIND RF NPS 4 CL150 SA-105	2		50006153
10	BRIDA BLIND RF NPS 32 -# 150 A SA105	1		50047181
9	BRIDA BLIND RF NPS 2 CL150 SA105	4		50009812
8	BRIDA BLIND NPS 20 CL150 SA-105	1		50008504
7	ARANDELA PLANA Ø7/8" DIN 125 AC BICR	16		50025362
6	ARANDELA PLANA Ø5/8" SA-F436 BIC	64		50016373
5	ARANDELA PLANA Ø1½" DIN 125 AC BICR	56		50025363
4	ARANDELA PLANA Ø1 1-8 SA-F436 BIC	40		50020850
3	ARANDELA GROWER Ø3/8" DIN 127 AC GALV	19		50003560
2	ANGULO 1½" X ¼" 3.44KG/M	1,458 m		10000042
1	ANGULO 1" X 3/16" 1.77KG/M	1,200 m		10000163
ITEM	DESCRIPCION	CANT.	OBSERVACION	SAP

LISTA DE MATERIALES