




PESO APROXIMADO: 7 TON

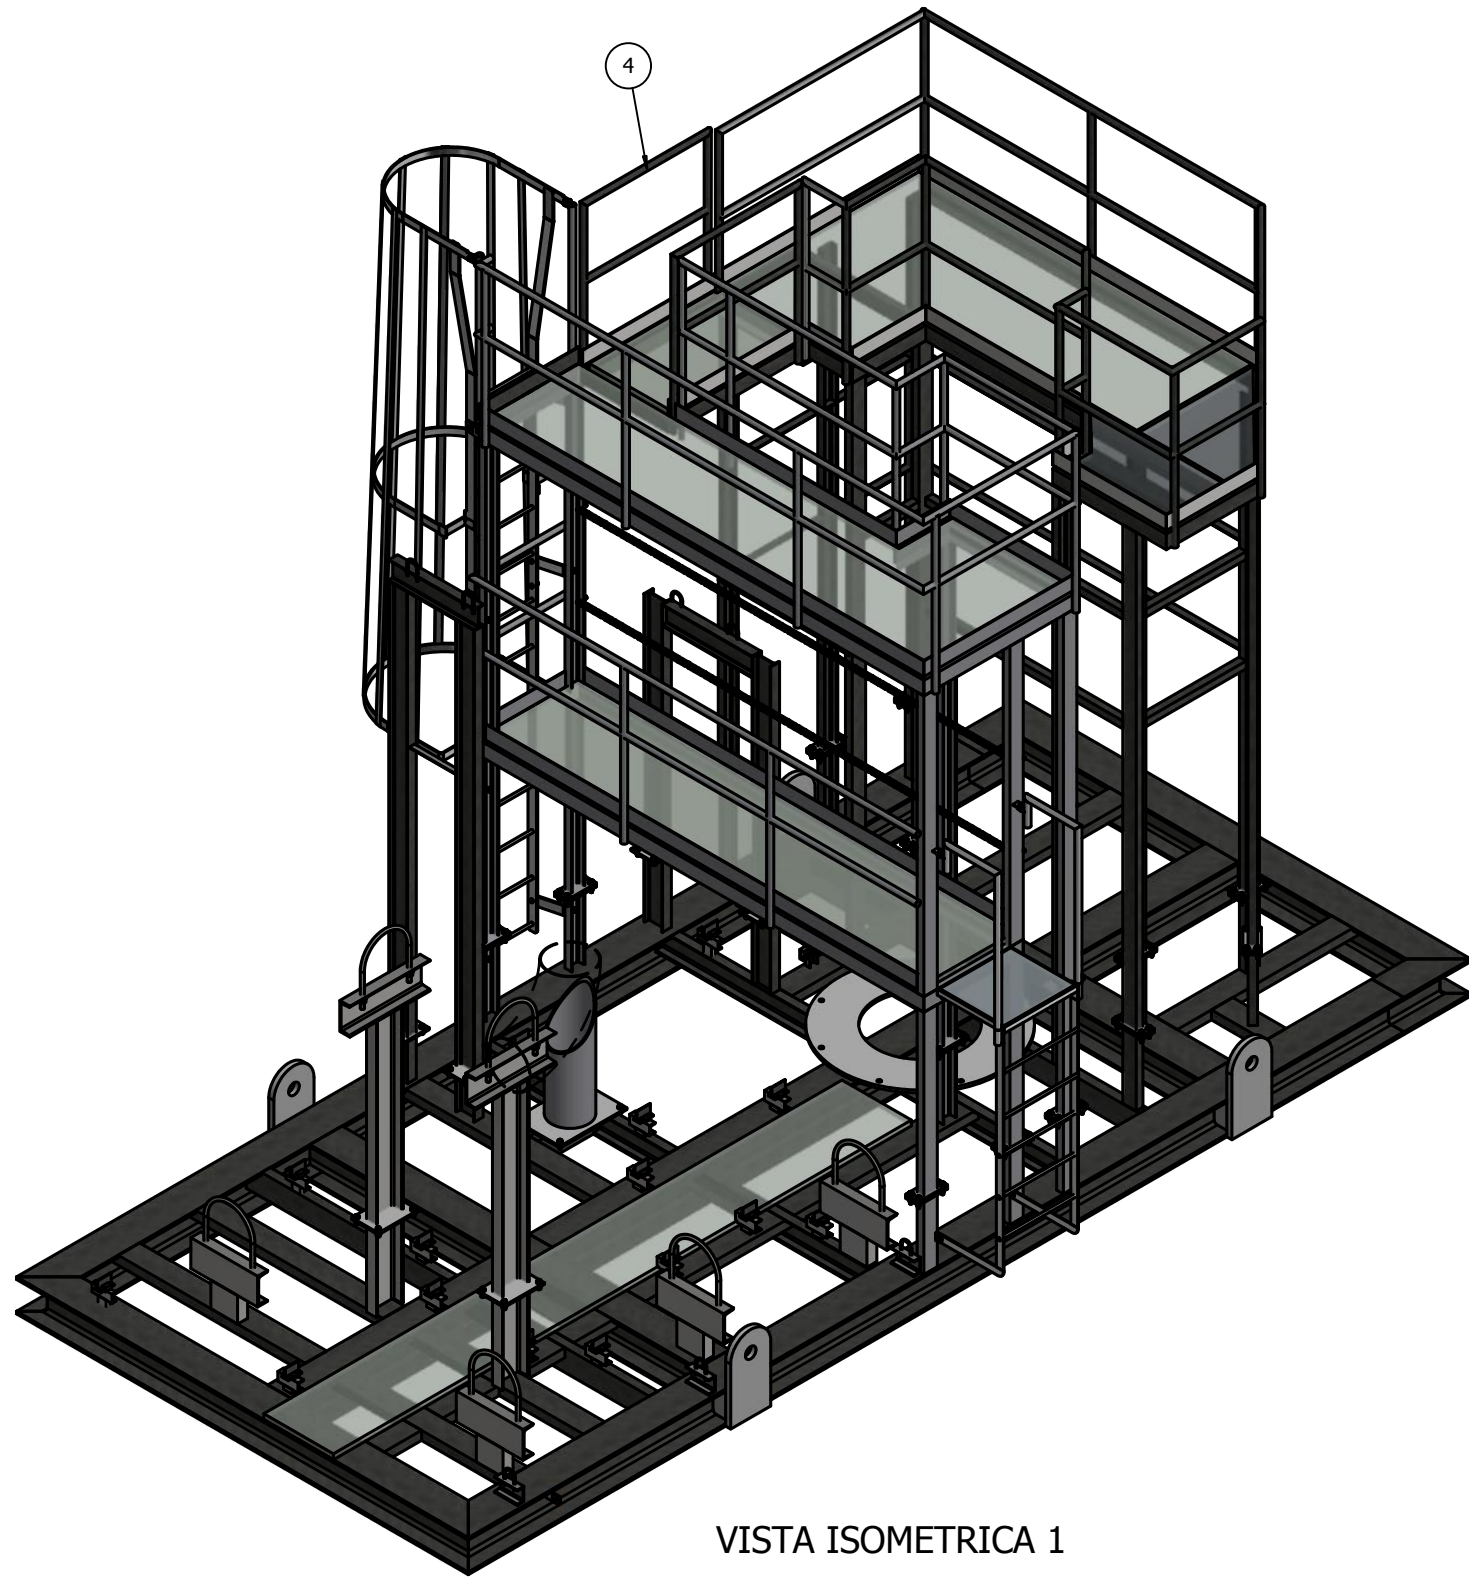


VISTA ISOMETRICA 1
ESCALA:(1 : 40)

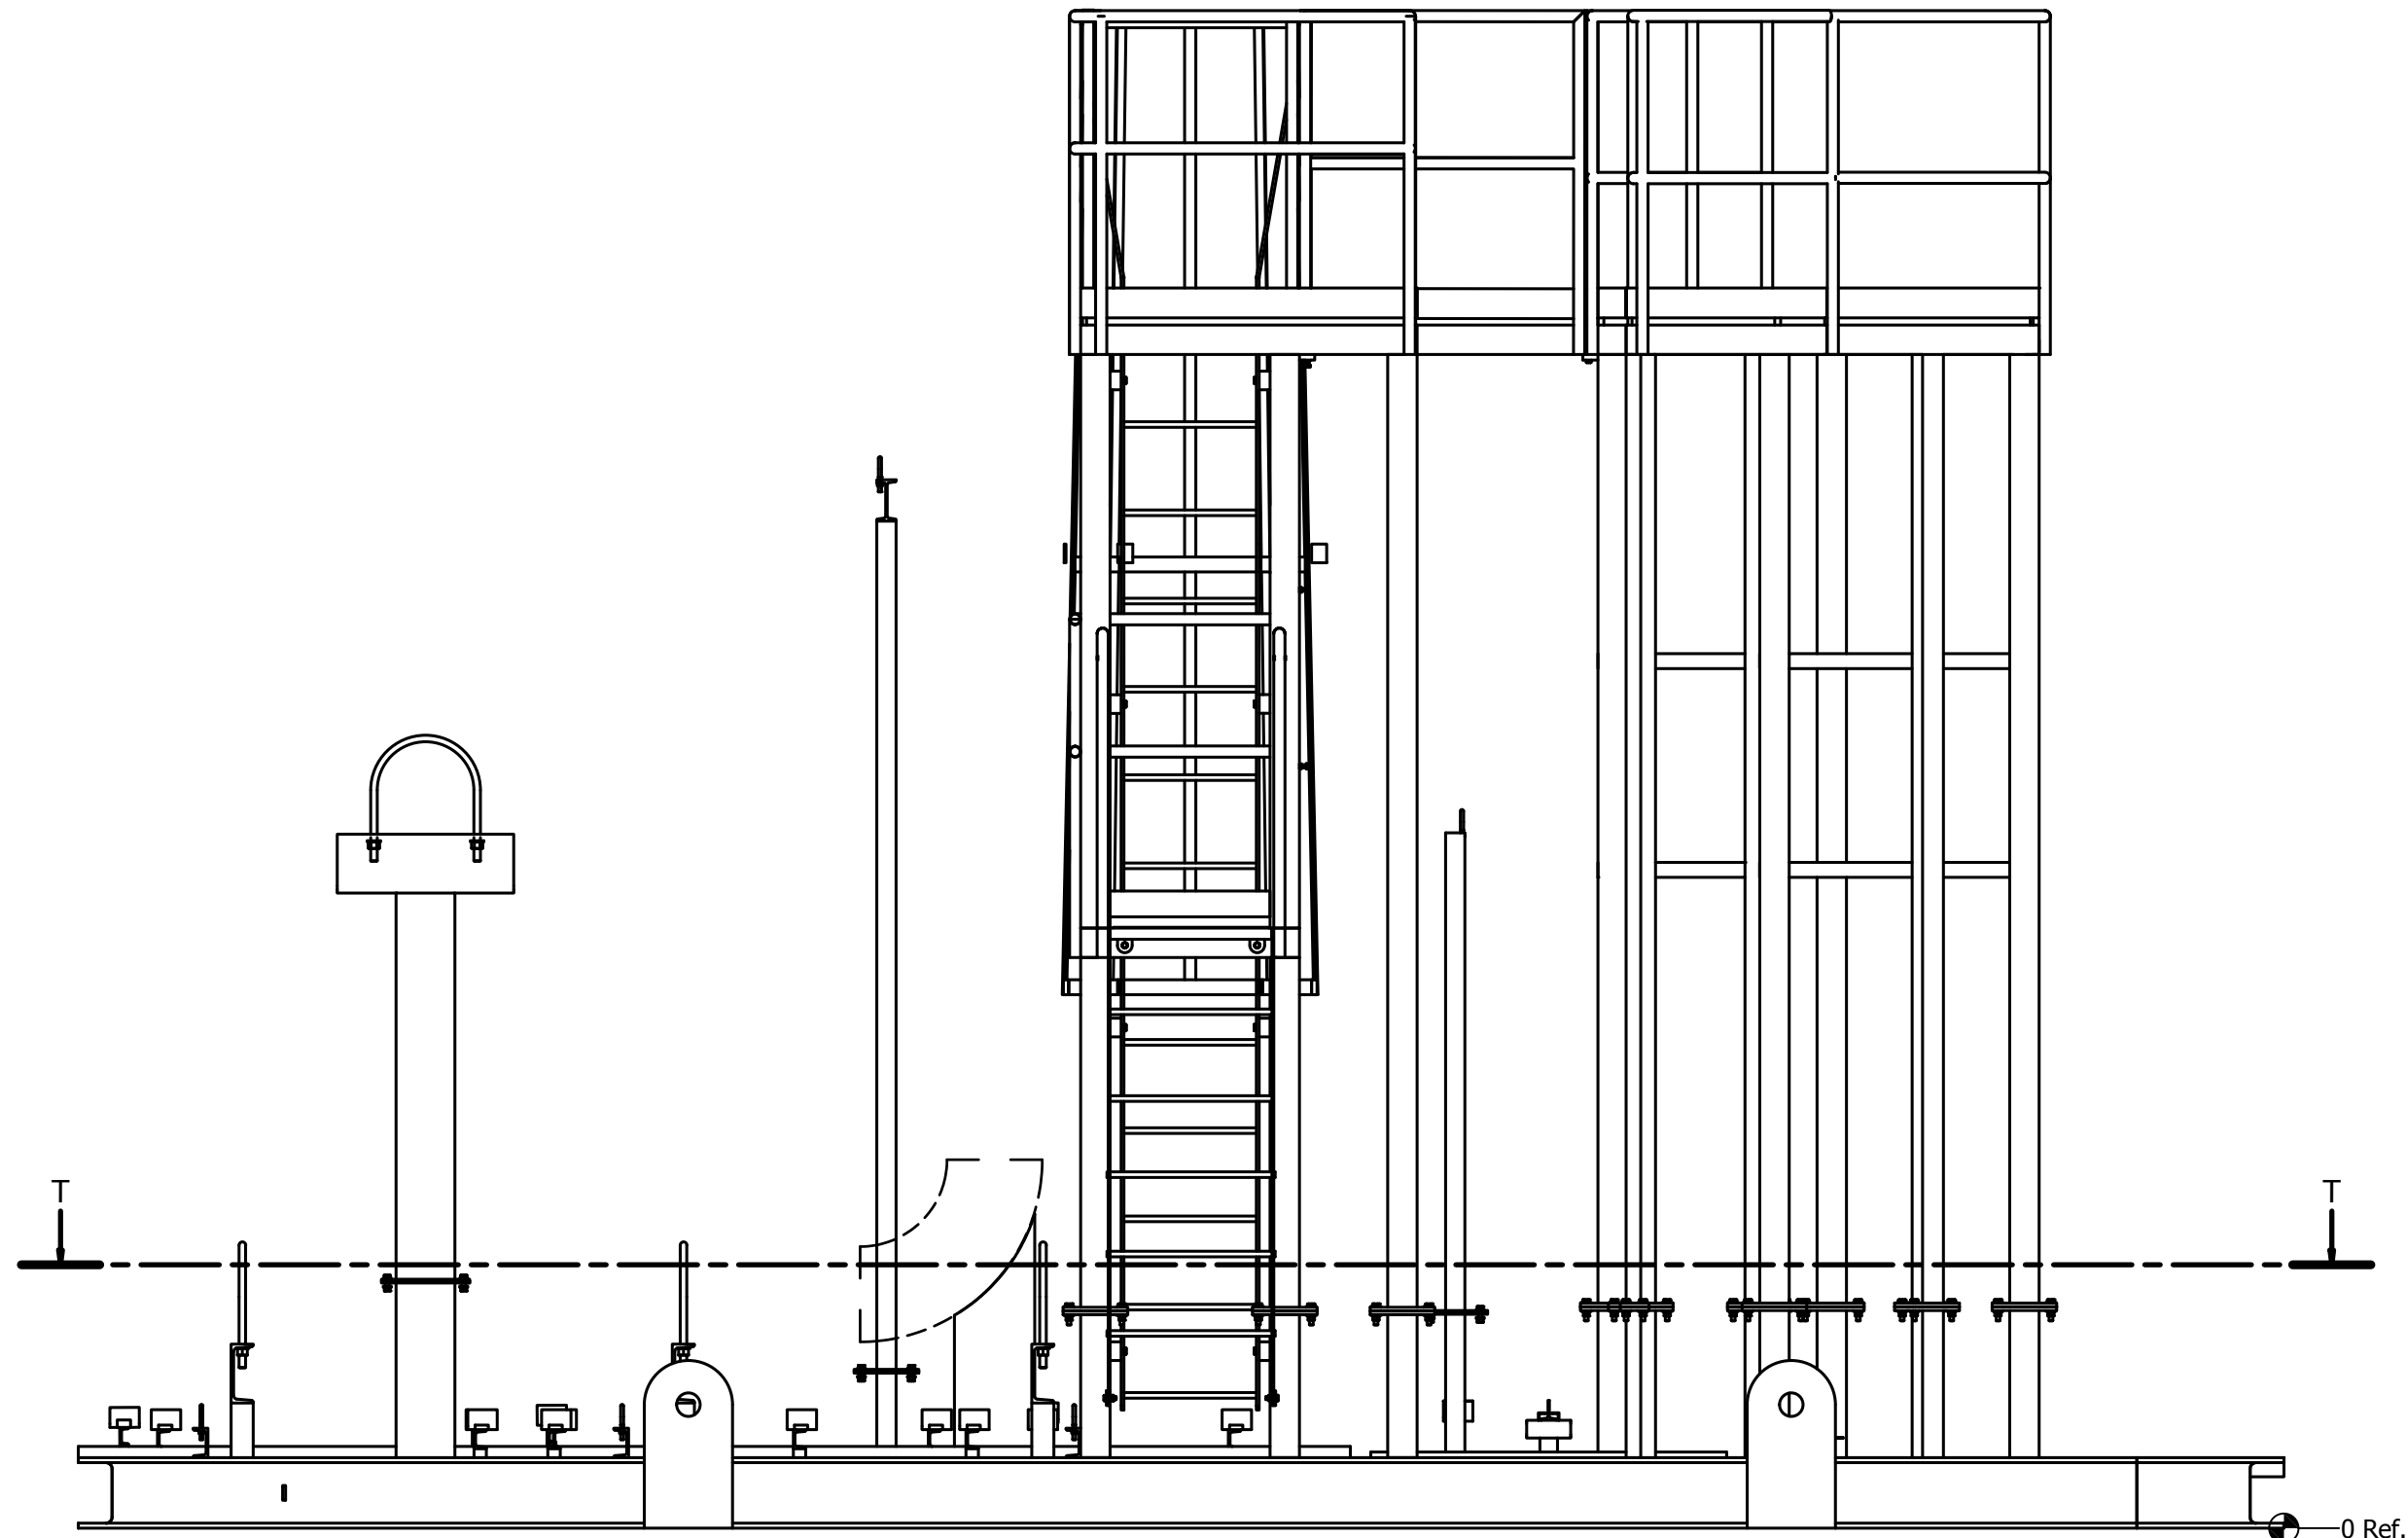


VISTA FRONTAL
ESCALA:(1 : 25)

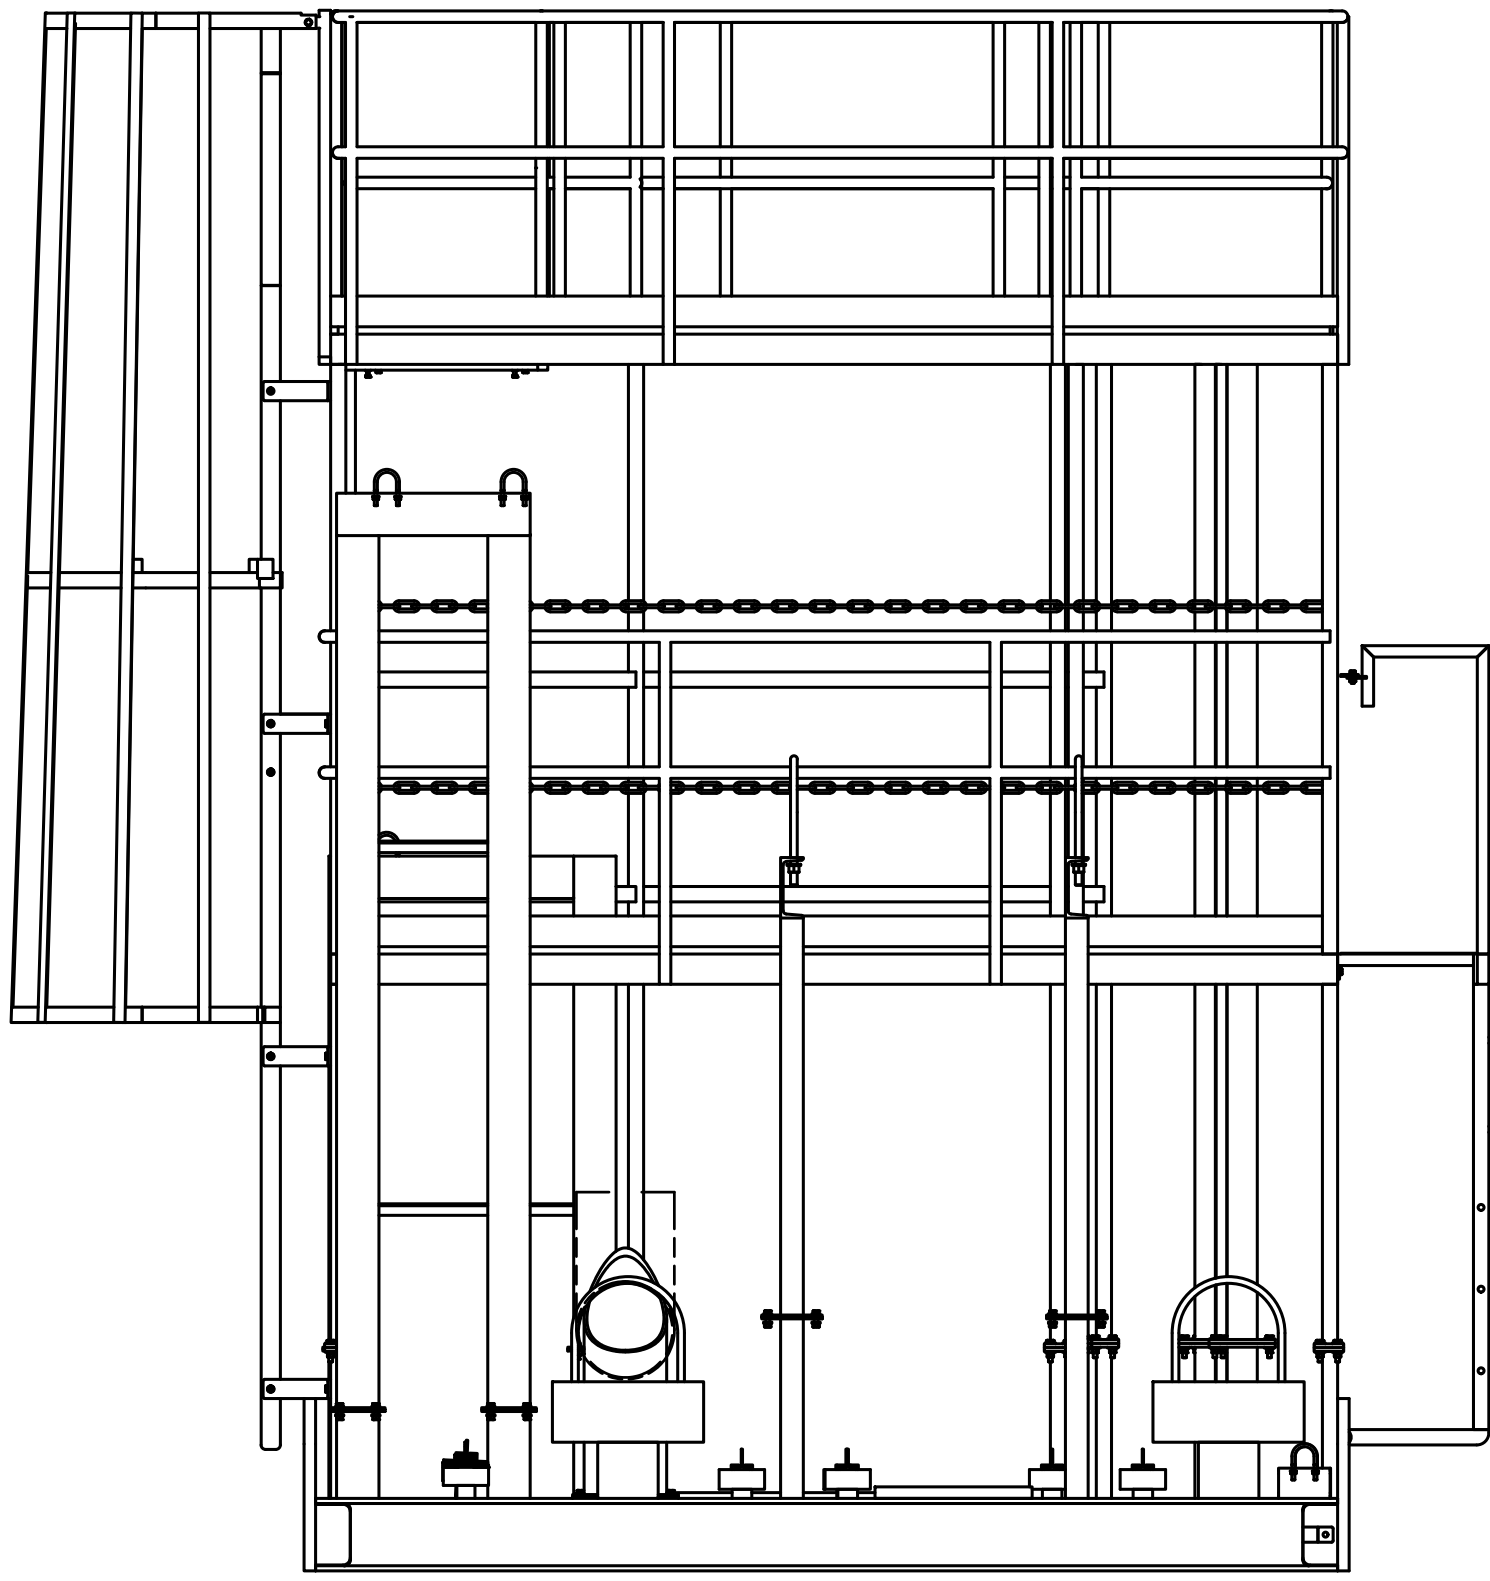


VISTA LATERAL IZQUIERDA
ESCALA:(1 : 25)

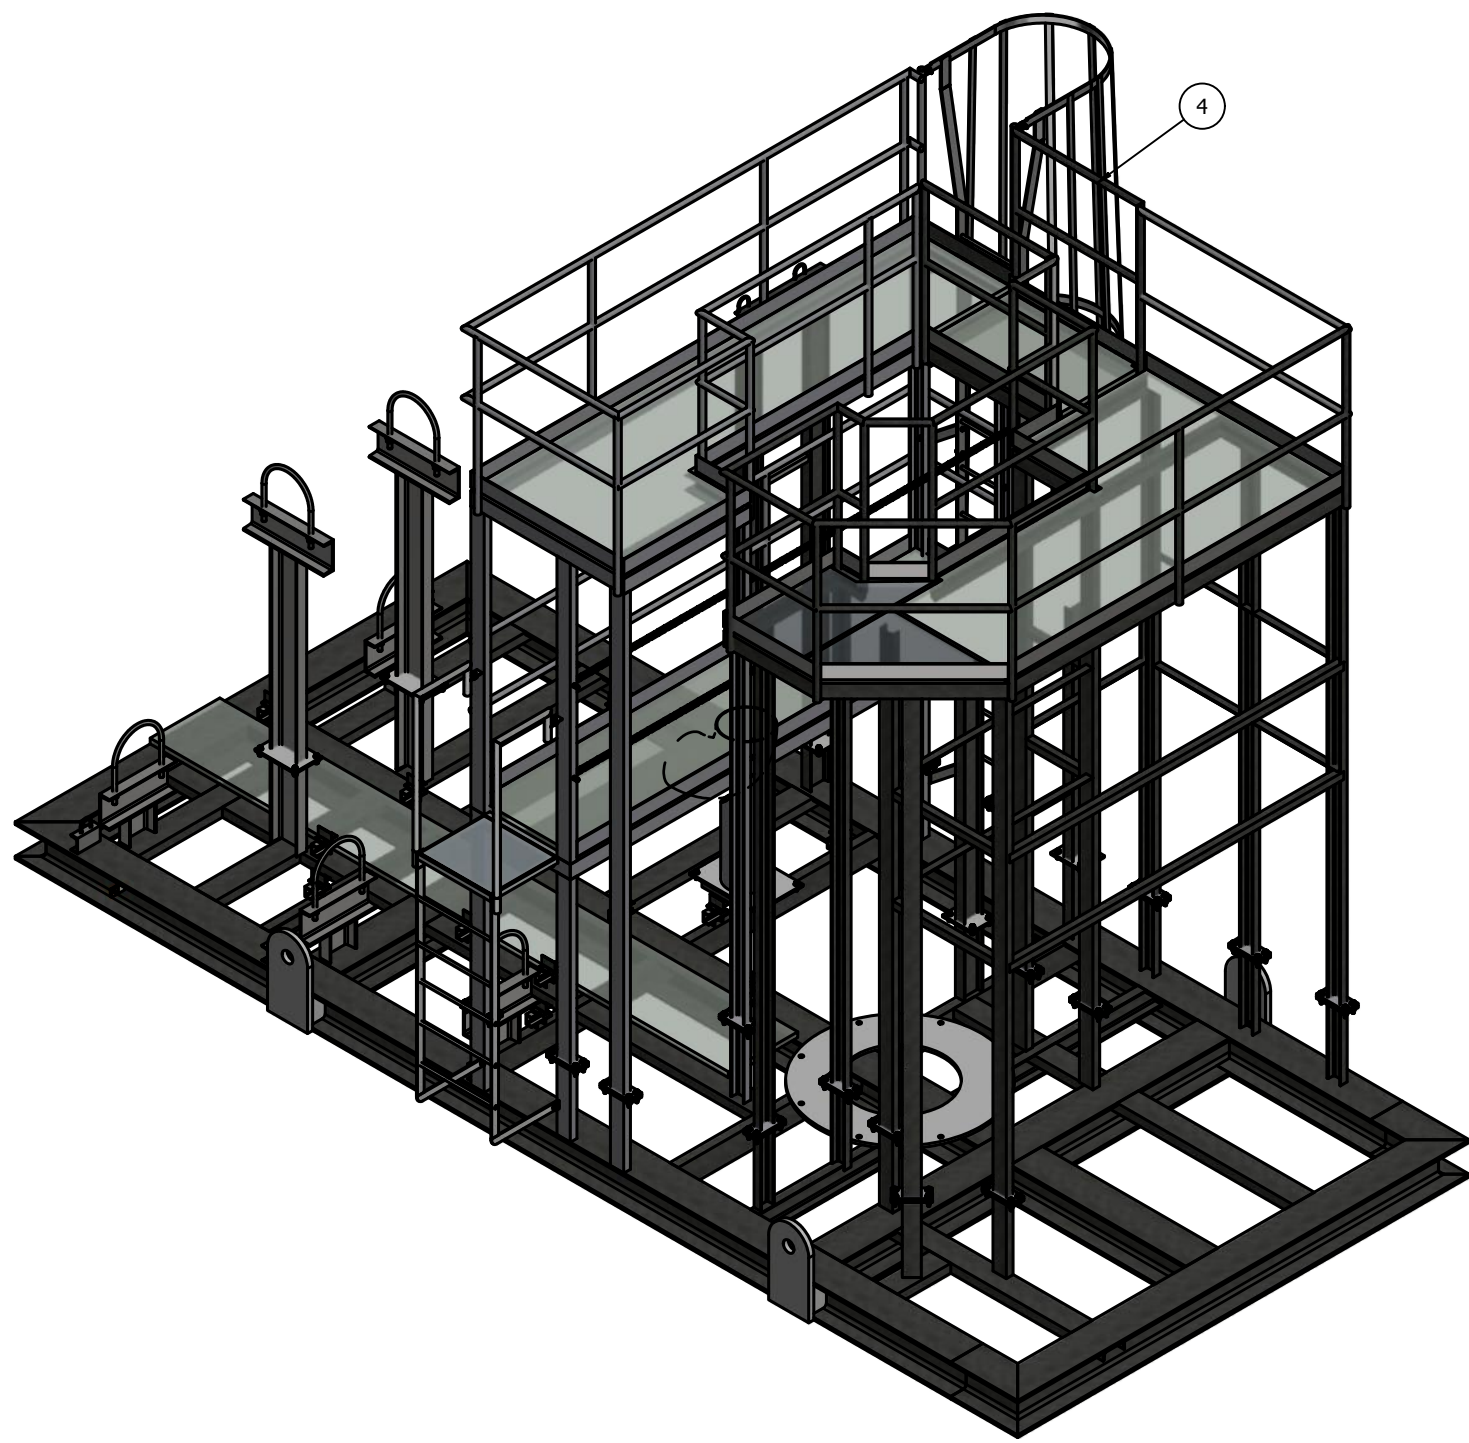

VISTA ISOMETRICA 2
ESCALA:(1 : 40)

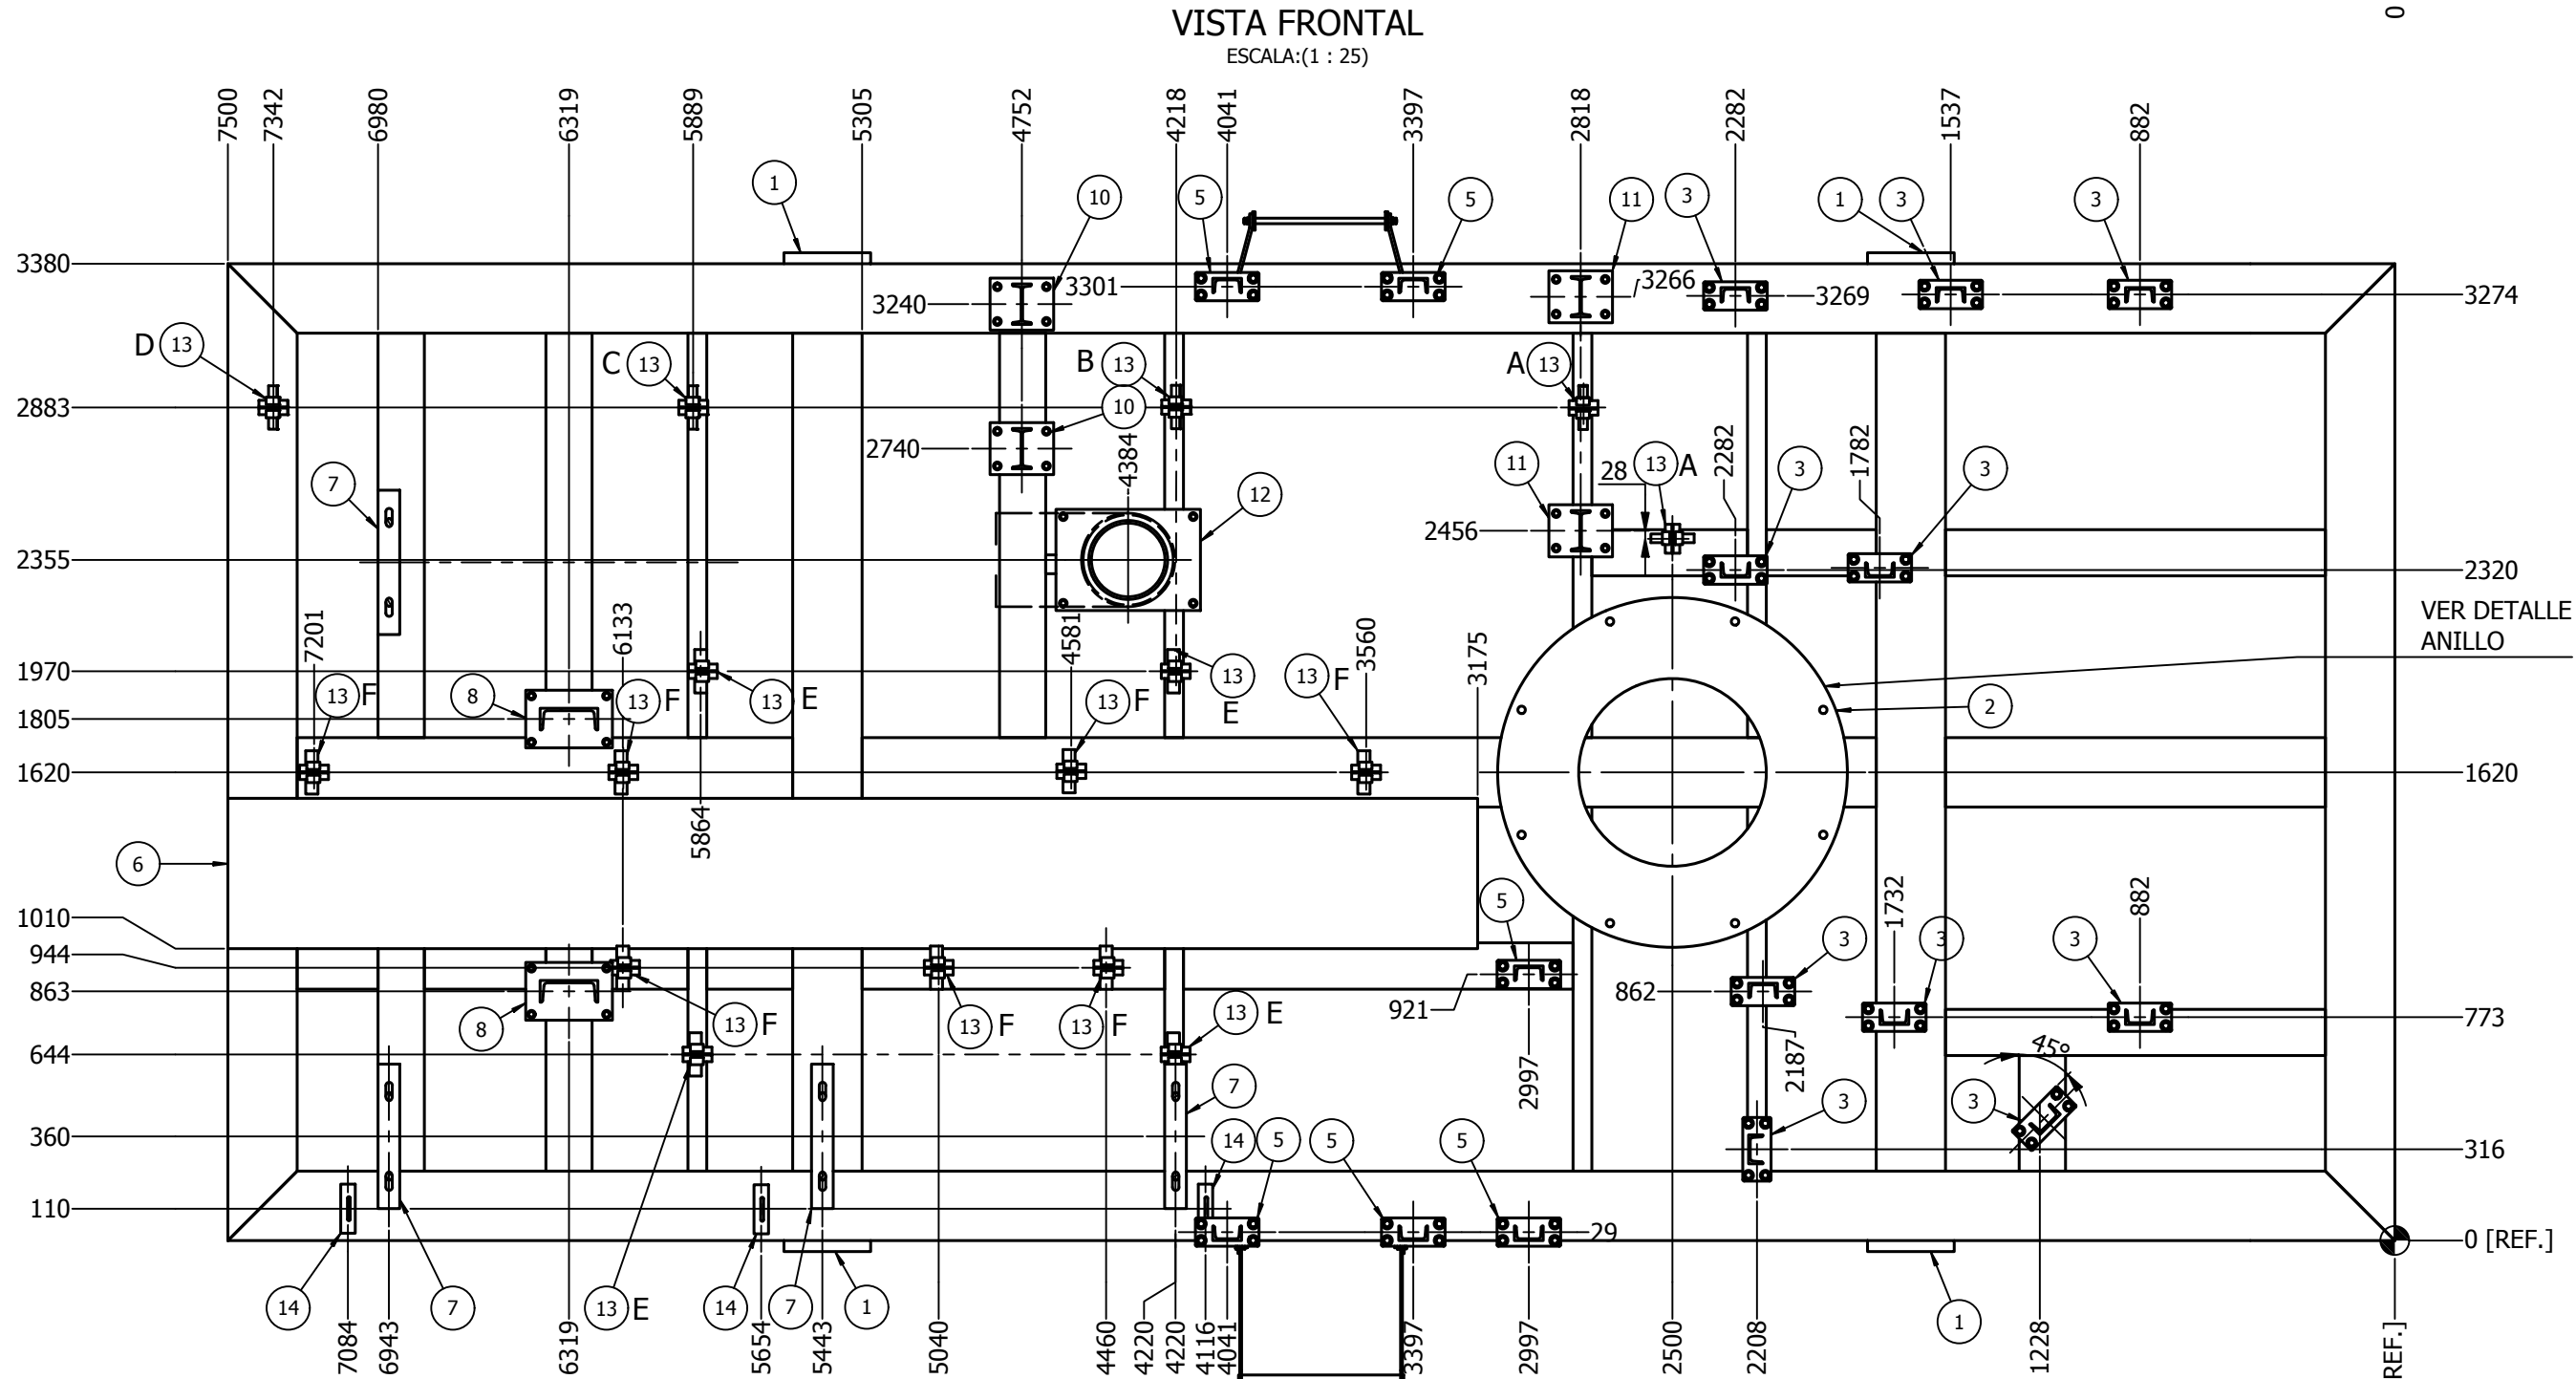

CORTE T-T
ESCALA:(1 : 25)

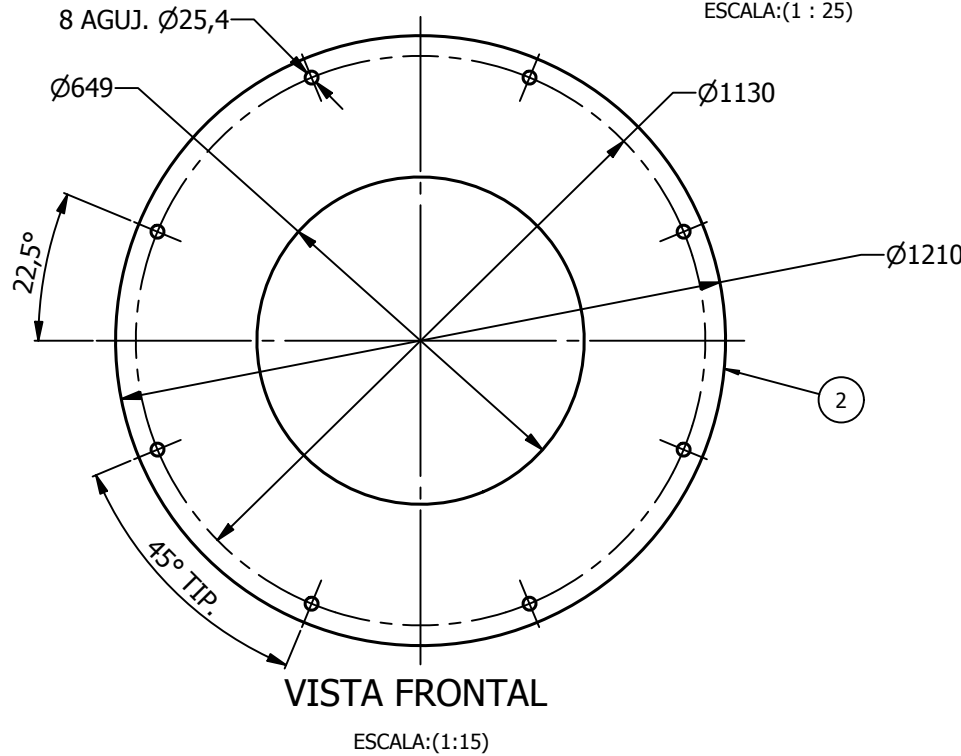


VISTA FRONTAL
ESCALA:(1:15)

NOTA: SOLDAR BASE A SKID DE ARRIBA Y ABAJO

14	SP-07	3	VER HOJA 3	
13	SP-06	16	VER HOJA 3	
12	SP-05	1	VER HOJA 3	
11	SP-04	1	VER HOJA 3	
10	SP-03	1	VER HOJA 3	
8	SP-01	2	VER HOJA 3	
7	SP-02	4	VER HOJA 3	
6	REJILLA TIPO TECHNOS GRIP LOCKED 3050 GALV.	2,249 m^2		50016423
5	ESTRUCTURA 3	1	VER PL 12765-EPG-M-PL-GE-003	
4	ESTRUCTURA 2	1	VER PL 12765-EPG-M-PL-GE-003	
3	ESTRUCTURA 1	1	VER PL 12765-EPG-M-PL-GE-003	
2	CHAPA 3/4" IRAM F26 150,7KG/M2	1,025 m^2		10002342
1	CÁNCAMO, IZAJE	4	VER HOJA 2	
ITEM	DESCRIPCION	CANT.	OBSERVACION	SAP

LISTA DE MATERIALES

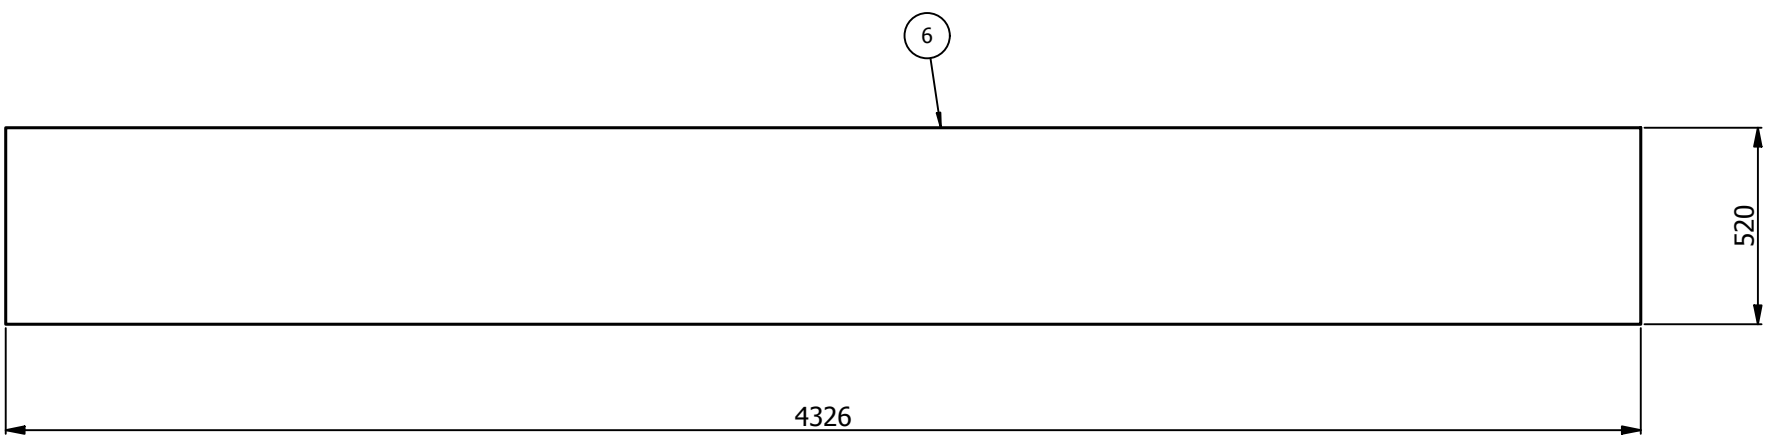


DETALLE REJILLA TECHNO
ESCALA:(1:20)

ESPECIFICACIONES DE SOLDADURAS	
ALTURA DE CORDÓN	0.7xMIN. ESPESOR A UNIR (SALVO INDICACIÓN)
TERMINACION:	1 CAPA - POLIUR. ALIFATICO - HEMPEL HEMPATANE HS 55610 - EPS: 50 a 70 micr. - 67% SÓLIDOS - SKID, SOPORTES. Y PLATAFORMA: NEGRO (RAL 9011) - ESCALERA. Y BARANDAS: AMARILLO RAL 1006.
INTERMEDIO:	1 CAPA - EPOXI ALTO SOLIDO - HEMPEL HEMPADUR 45880 - EPS: 100 A 150 micr.79% SÓLIDOS
BASE:	1 CAPA - CINC SILICATO DE ETILO - GALVOSIL 15700 - EPS: 50 a 100 micr. 62% SÓLIDOS
PREPARACION DE LA SUPERFICIE:	LIMPIEZA CON SOLVENTE, PARA ELIMINAR TODA TRASA DE GRASA O ACEITE AMOLADO Y SUAVIZADO DE CANTOS s/NACE STANDARD RPO 178-95 Gr.D CHORREADO ABRASIVO, GRADO LIMPIEZA: SSPC-SP 10-GRADO SA 2 1/2 - PERFIL 65-75 micr.
ESQUEMA DE PINTURA EXTERIOR - ESQUEMA 201 DE YPF	


TOLERANCIAS PARA CALDERERÍA - DIN 8570 (ISO 13920)													
DIMENSIONES CALIDAD		>2 a 30	>30 a 120	>120 a 400	>400 a 1000	>1000 a 2000	>2000 a 4000	>4000 a 8000	>8000 a 12000	>12000 a 16000	>16000 a 20000	>20000 —	
B		± 1	± 2	± 2	± 3	± 4	± 6	± 8	± 10	± 12	± 14	± 16	
FORMA Y POSICIÓN	TOL.	>30 a 120	>120 a 315	>315 a 1000	>1000 a 2000	>2000 a 4000	>4000 a 8000	>8000 a 12000					
	DINER.	± 1.5	± 3	± 5.5	± 9	± 11	± 16	± 20					
									ANGULOS	LADO MAS CORTO			
									TOL.	± 13 mm/m	>6 a 315	>315 a 1000	>1000 a 4000
											± 9 mm/m	± 6 mm/m	
NOTAS													
1- SE REQUIEREN SOLDADORES CALIFICADOS.													
2- SOLDADURA DE RESPALDO ESTA PERMITIDA SI SE REQUIERE Y LA JUNTA ES ACCESIBLE													
ALTURA CORDÓN		TOPE: PENETRACION TOTAL. FUSION COMPLETA. FILETE: 0,7xMIN. ESPESOR A UNIR (SALVO INDICACIÓN)											
METODO		TIP.: DE CATETO (RESTO VER TÍPICO PARTICULARES)											
SIMBOLOGIA		SEGÚN AWS 2.4											
ESPECIFICACIONES DE SOLDADURAS													

SKID
PESO APROXIMADO: 4TN


CANT.: 1
COLOR: Negro Ral 9011

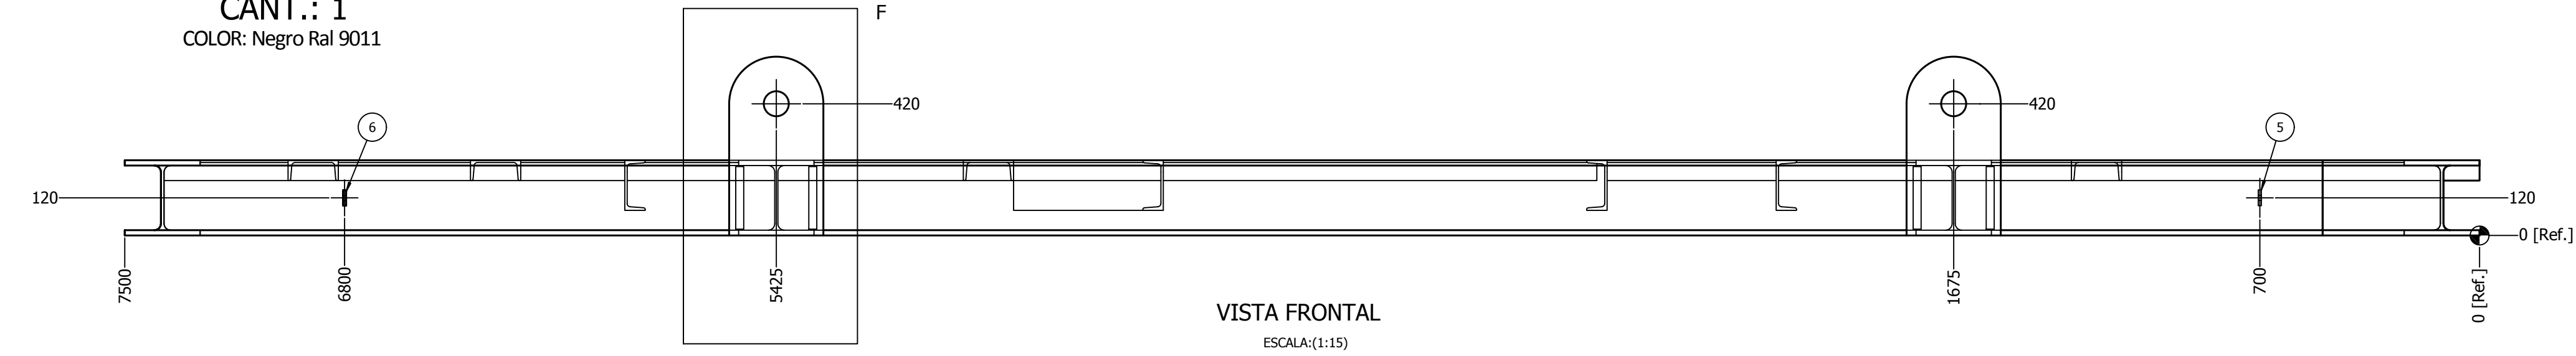


VISTA FRONTAL
ESCALA:(1:15)

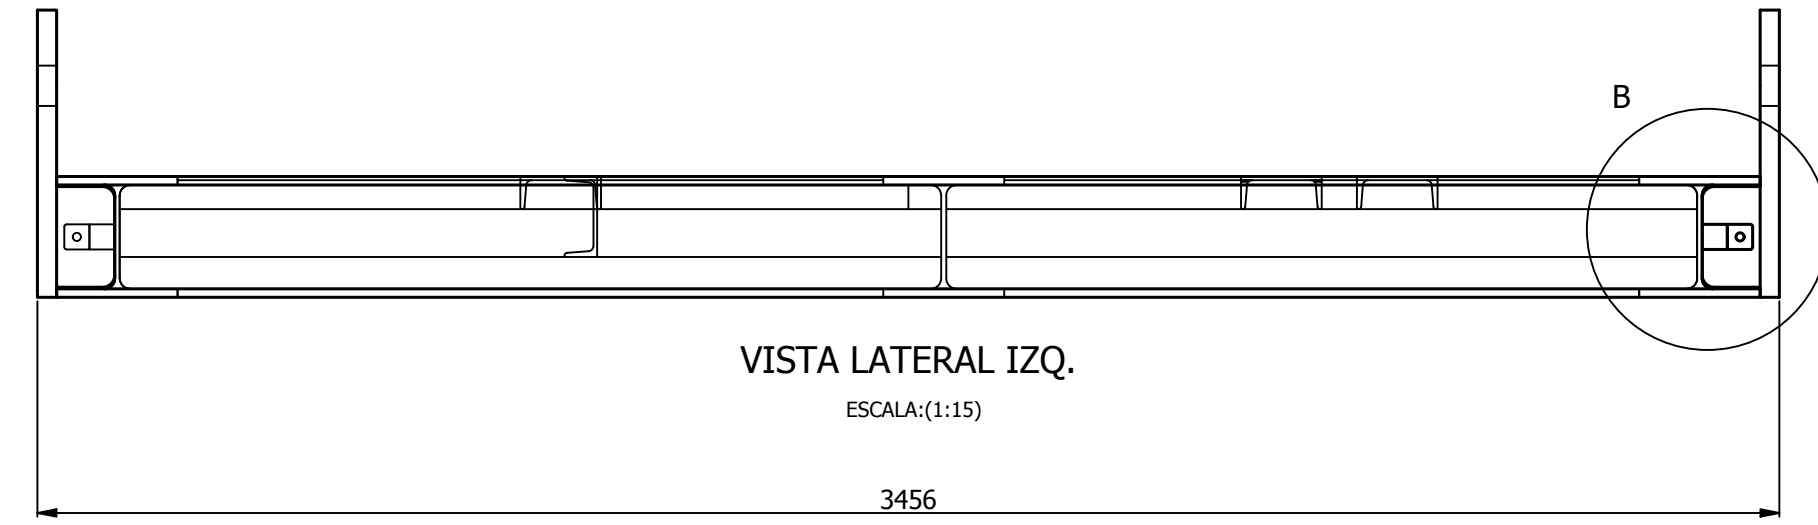

VISTA LATERAL IZQ.
ESCALA:(1:15)

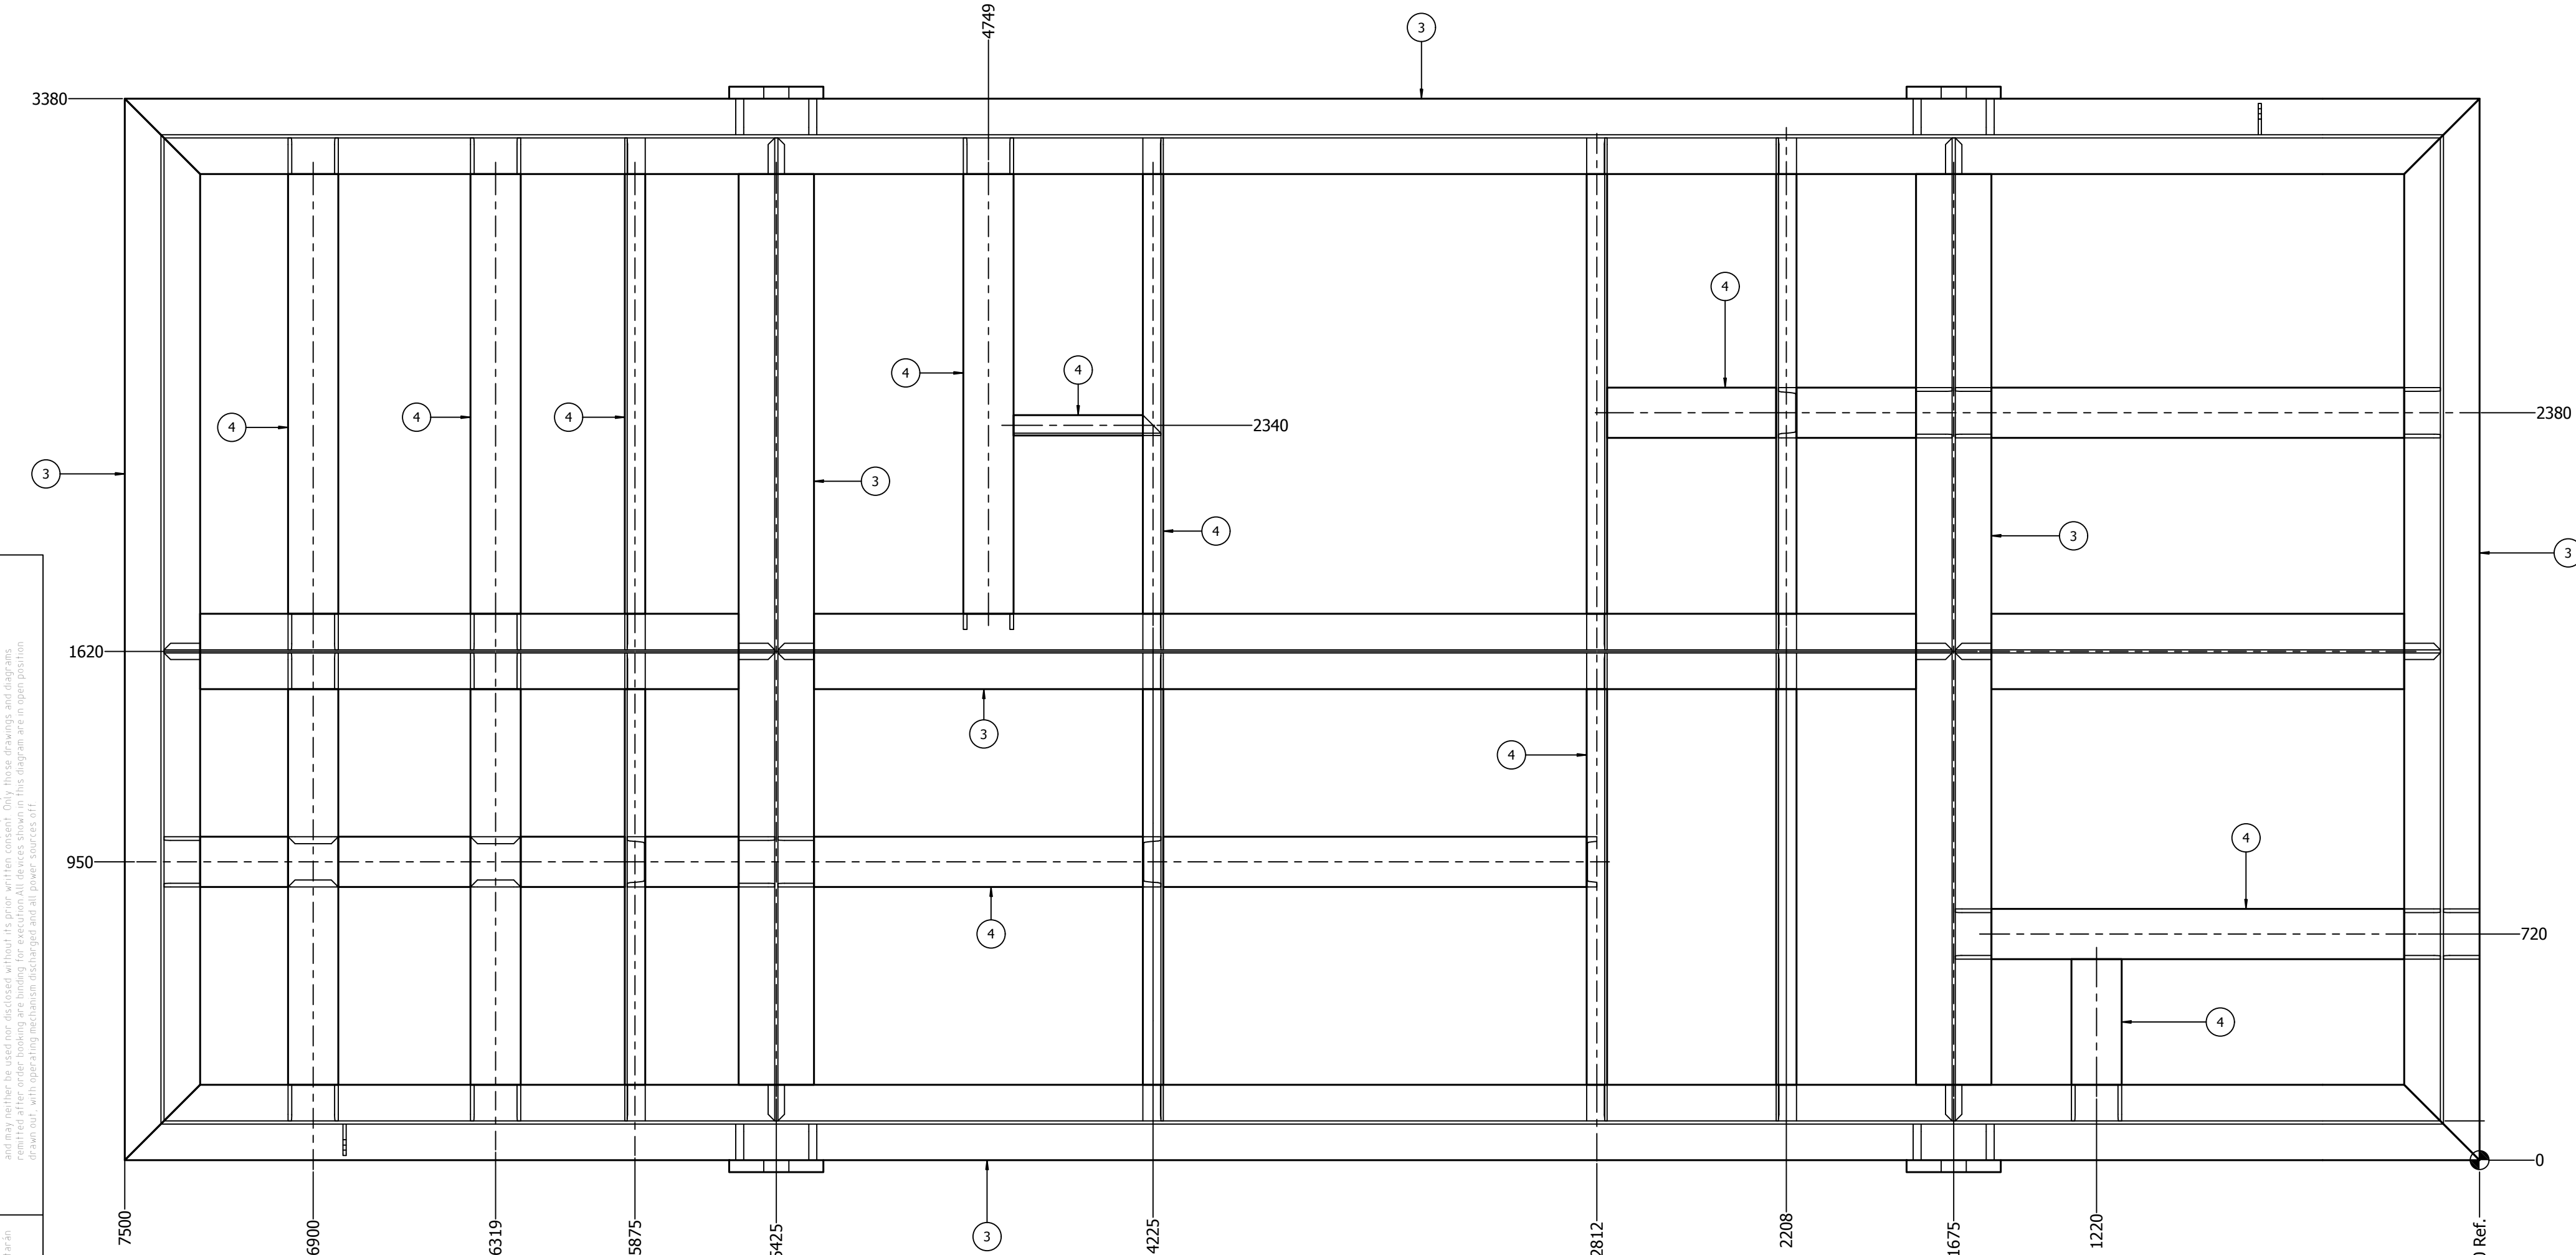

VISTA SUPERIOR
ESCALA:(1:15)

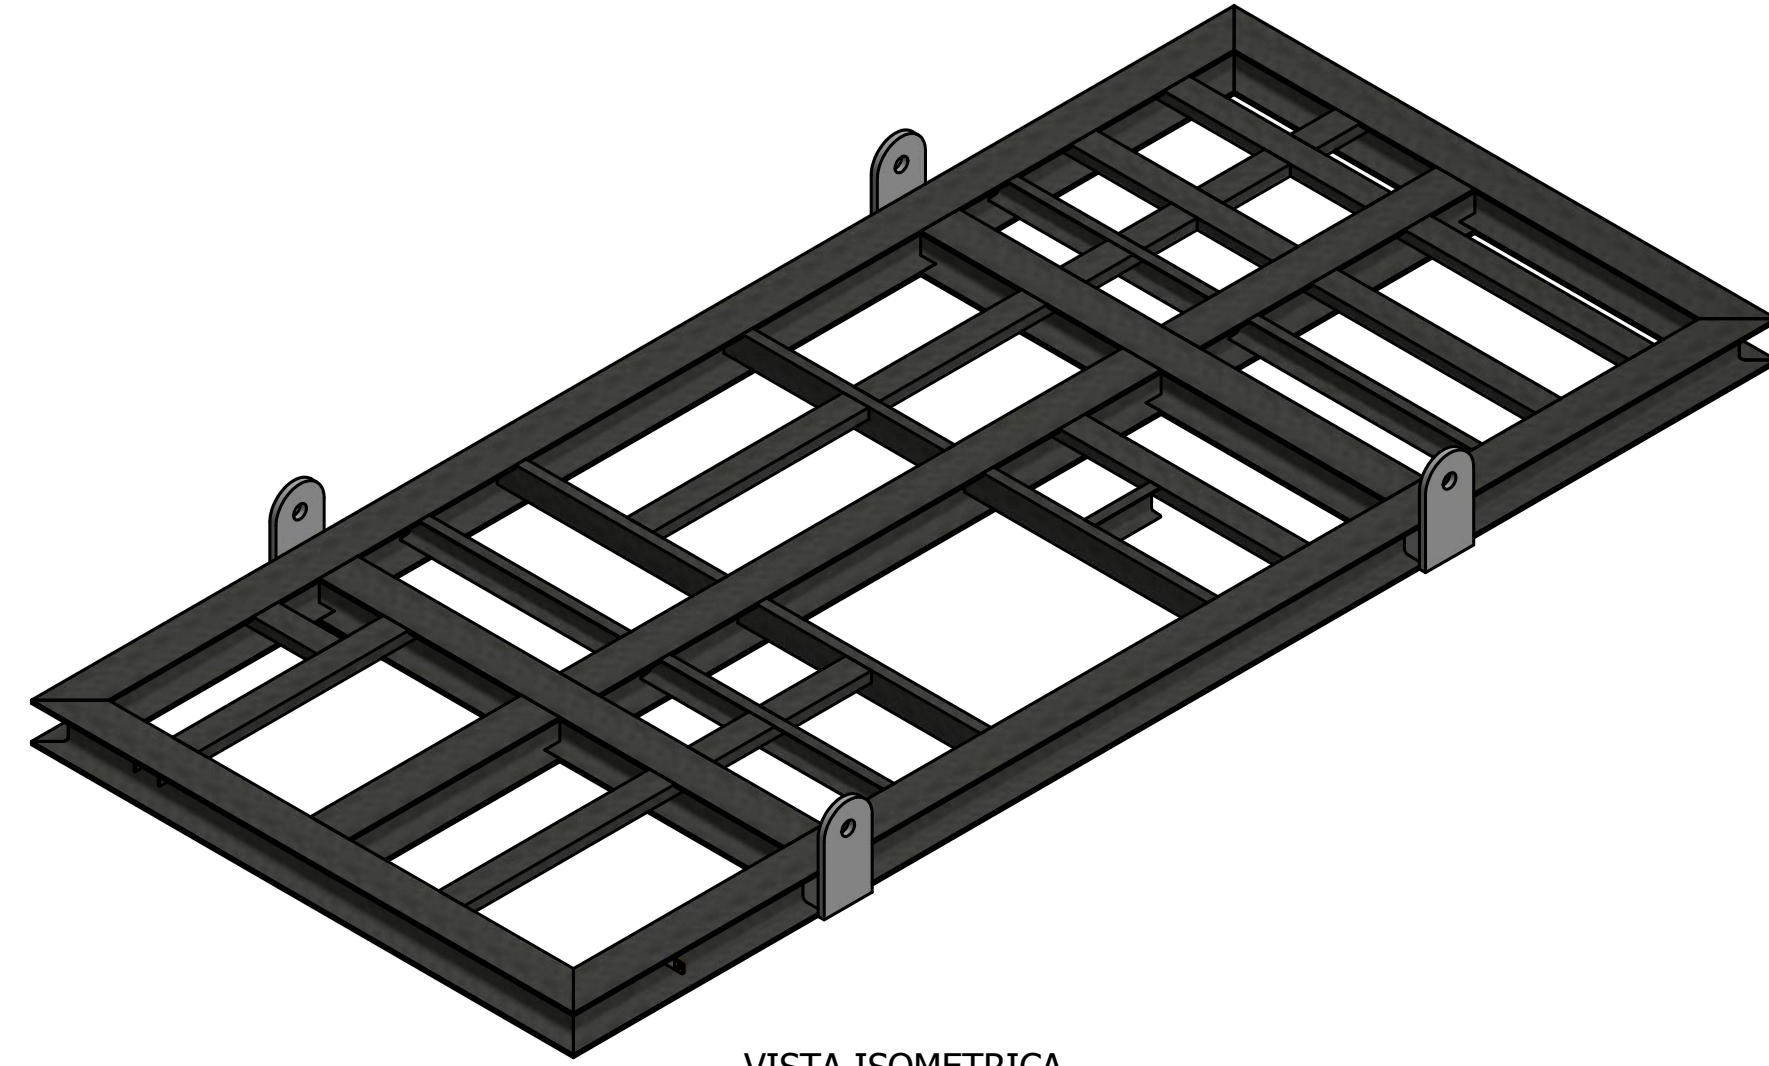


VISTA ISOMETRICA
ESCALA:(0,03 : 1)


NOTAS: 1)REALIZAR ENSAYO TINTAS PENETRANTES O PARTICULAS MAGNETICAS EN CANCAMOS DE IZAJE
2) AMOLAR CANTOS VIVOS
3)SE RESPETARAN LAS DIMENSIONES ACOTADAS, LAS DIMENSIONES DADAS EN EL LISTADO DE MATERIALES SON SOLO DE REFERENCIA.

6	PLANCHUELA COBRE ELECTROLITICO 50X10MM	2	10000901
5	PLANCHUELA 2" X 3/8" 3.80KG/M	0,100 m	10000031
4	PERFIL UPN 160 18.80 KG/M	30,222 m	10000054
3	PERFIL HEB 240 83.20Kg/m	35,270 m	10002730
2	CHAPA 1 1/2" IRAM F26 301,4KG/M2	0,756 m^2	10000258
1	CHAPA 1" IRAM F26 200,9KG/M2	0,184 m^2	10002314

NOTAS	
1- SE REQUIEREN SOLDADORES CALIFICADOS.	
2- SOLDADURA DE RESPALDO ESTA PERMITIDA SI SE REQUIERE Y LA JUNTA ES ACCESIBLE	
ALTURA CORDÓN	TOPE: PENETRACION TOTAL. FUSION COMPLETA. FILETE: 0,7xMIN. ESPESOR A UNIR (SALVO INDICACIÓN)
METODO	TIP.: DE CATETO (RESTO VER TÍPICO PARTICULARES)
SIMBOLOGIA	SEGÚN AWS 2.4
ESPECIFICACIONES DE SOLDADURAS	
ESPECIFICACIONES DE SOLDADURAS	
ALTURA DE CORDÓN 0,7.xMIN. ESPESOR A UNIR (SALVO INDICACIÓN)	
TOLERANCIAS PARA CALDERERÍA - DIN 8570 (ISO 13920)	
DIMENSIONES CALIDAD	
B	
TOL.	

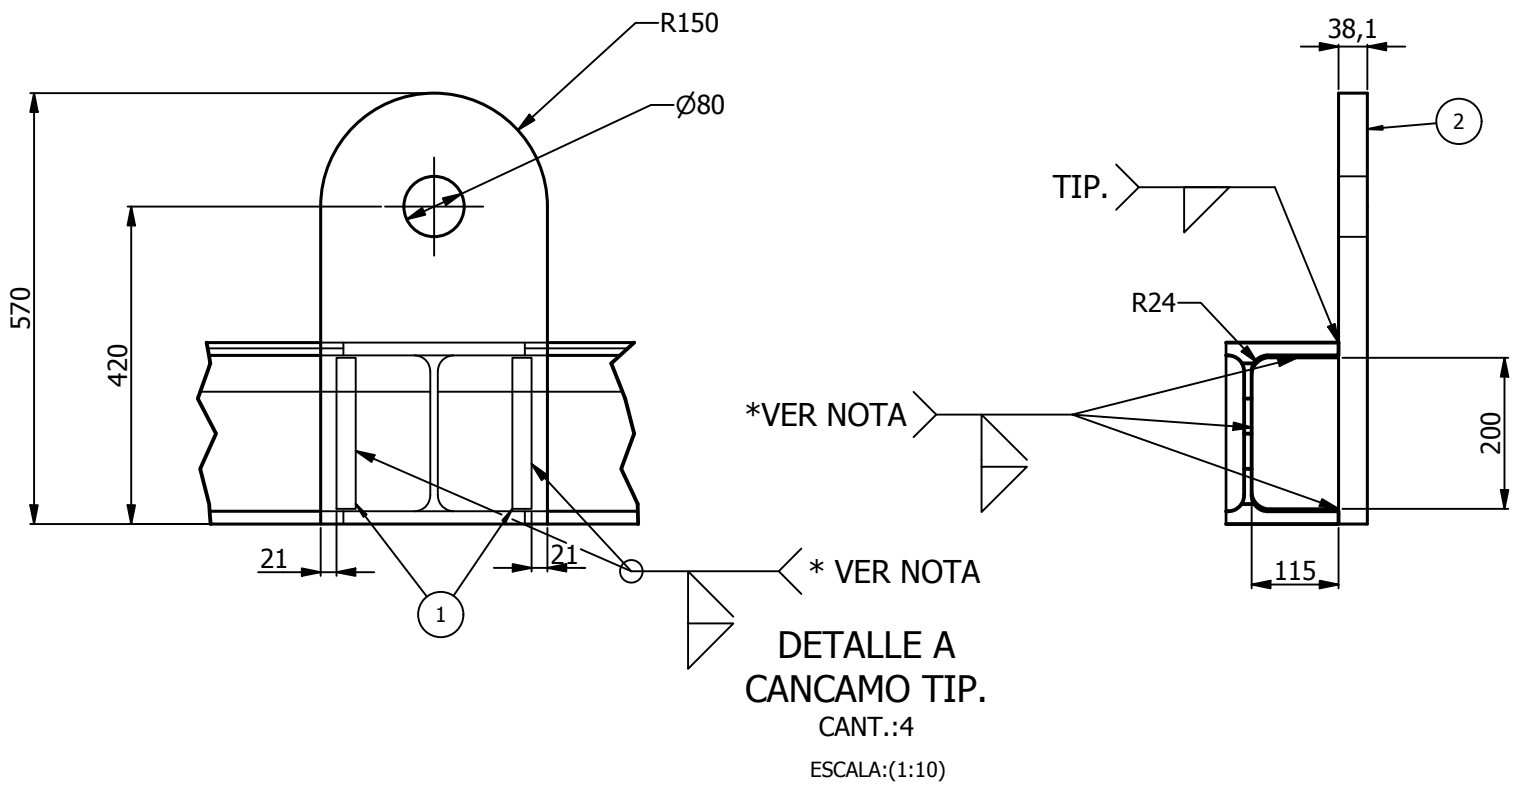

DETALLE A
CANCAMO TIP.
CANT.:4
ESCALA:(1:10)

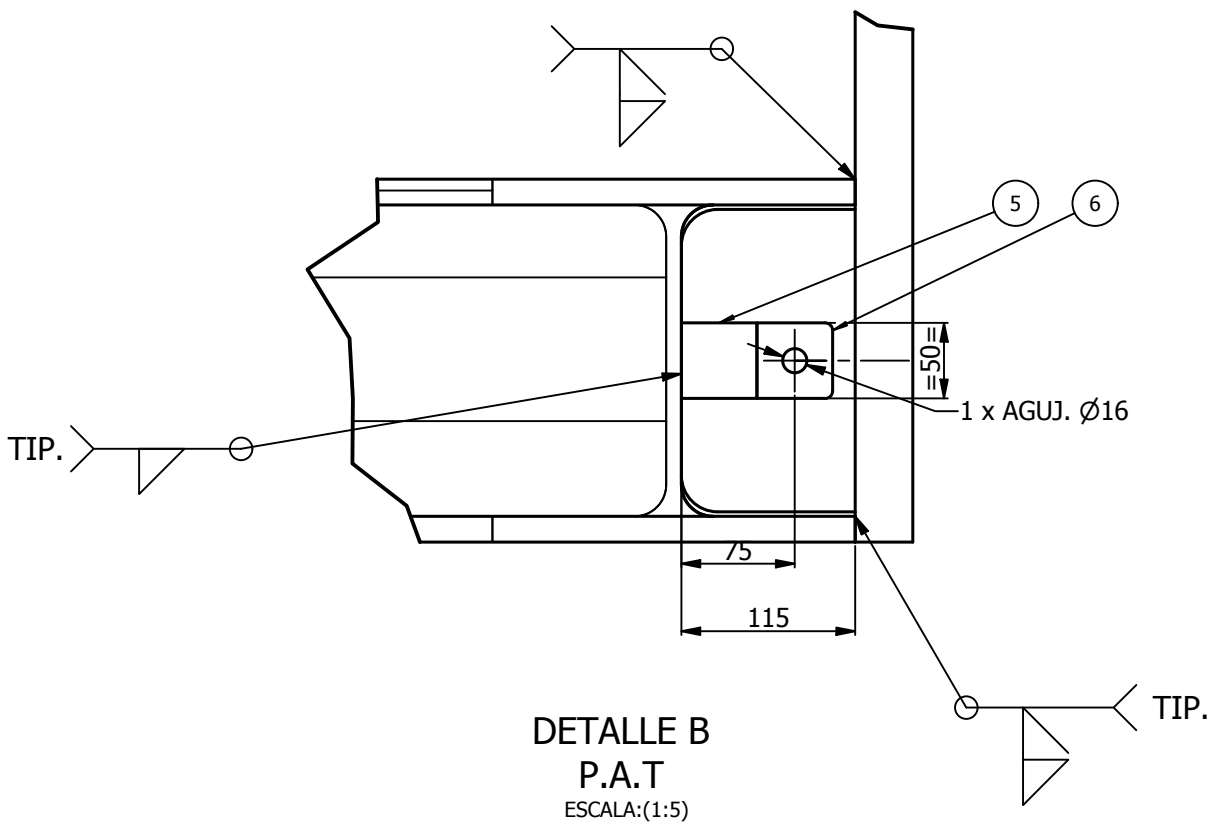


DETALLE B
P.A.T
ESCALA:(1:5)

SP-01


CANT.: 2

COLOR: Negro Ral 9011

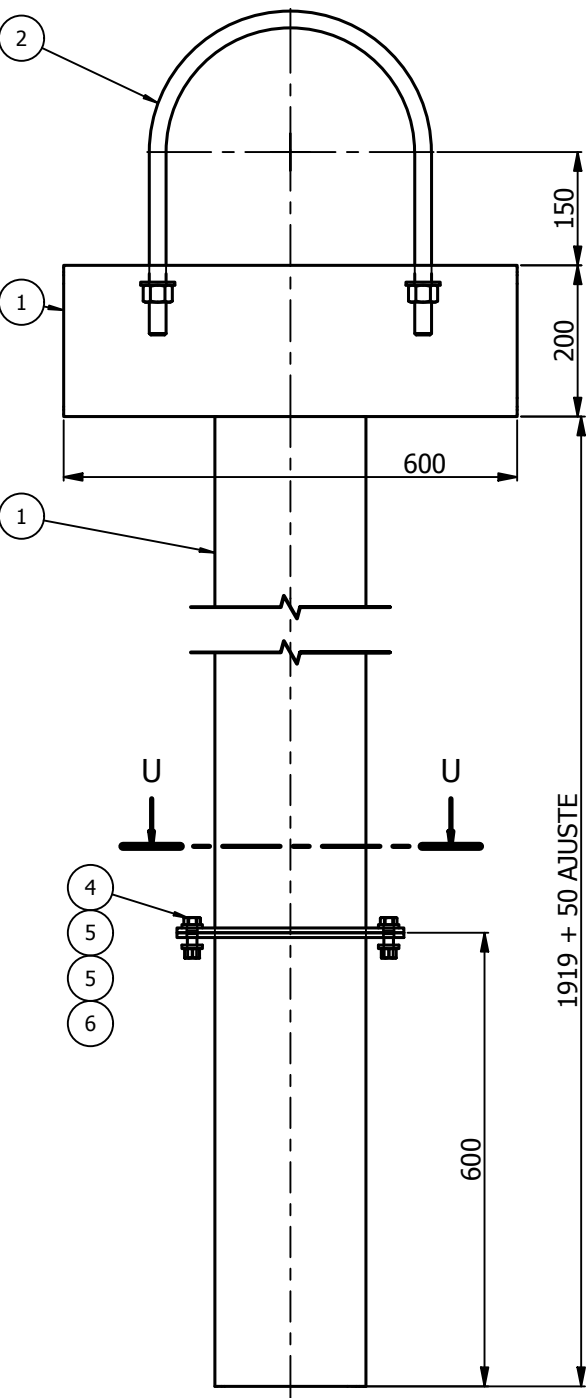


VISTA FRONTAL

ESCALA:(1:10)

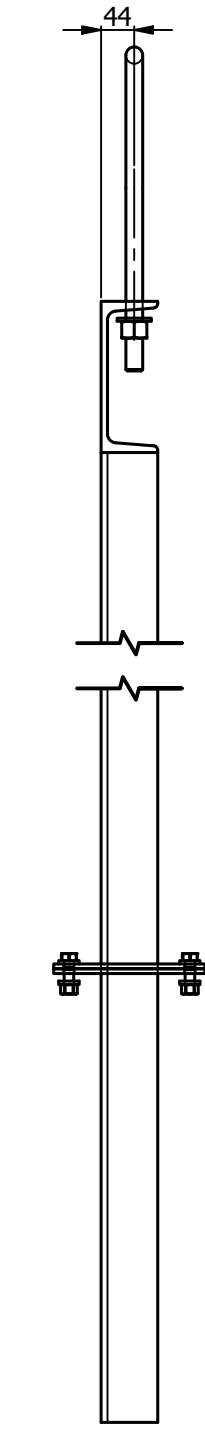

VISTA LATERAL

ESCALA:(1:10)

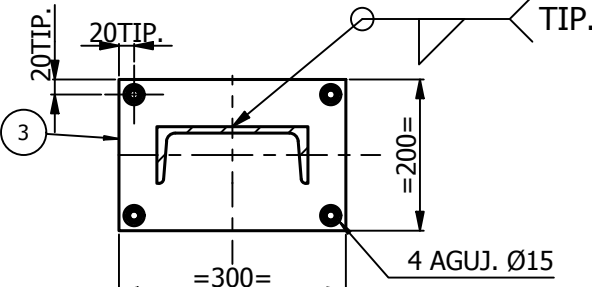

CORTE U-U

ESCALA:(1:10)

NOTA: LISTA DE MATERIALES PARA UNA UNIDAD


6	TUERCA HEX UNC ½ DIN934 AC GALV	4		50003934
5	ARANDELA PLANA Ø½ SA-F436 BIC	8		50016372
4	BULON H UNC ½" x 1¾" DIN931 SAE-5 BICR	4		50004980
3	CHAPA ¼" IRAM F26 50,3KG/M2	0,120 m^2		10002270
2	U-BOLT 12 C_TUERCAS Y ARAND 7_8 BRICR	1		50014795
1	PERFIL UPN 200 25.30 KG/M	2,519 m		10000194
ITEM	DESCRIPCION	CANT.	OBSERVACION	SAP

LISTA DE MATERIALES

SP-07


CANT.: 3

COLOR: Negro Ral 9011

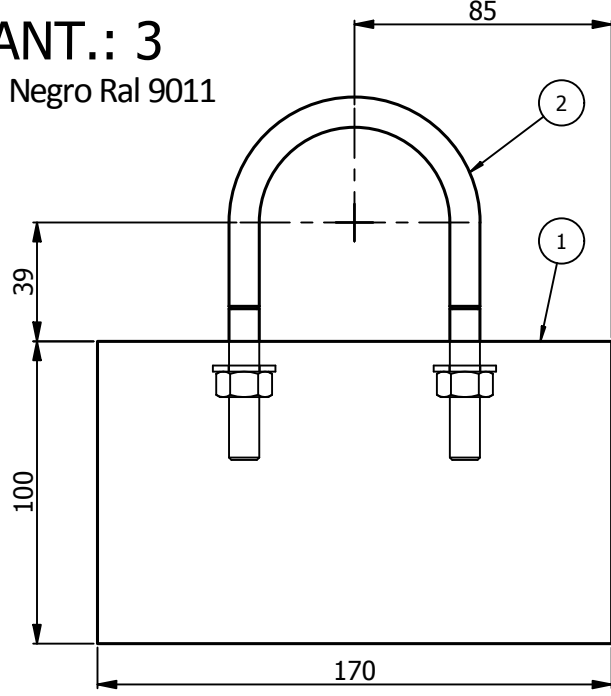

VISTA FRONTAL

ESCALA:(1 : 2.5)

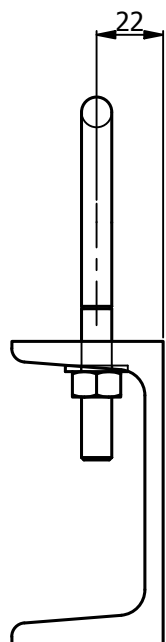

VISTA LATERAL

ESCALA:(1 : 2.5)

NOTA: LISTA DE MATERIALES PARA UNA UNIDAD


2	U-BOLT 2 HPG° CON TUERCAS Y ARANDELAS	1		50006170
1	PERFIL UPN 100 10.60 KG/M	0,17 m		10000192
ITEM	DESCRIPCION	CANT.	OBSERVACION	SAP

LISTA DE MATERIALES

SP-02


CANT.: 4

COLOR: Negro Ral 9011

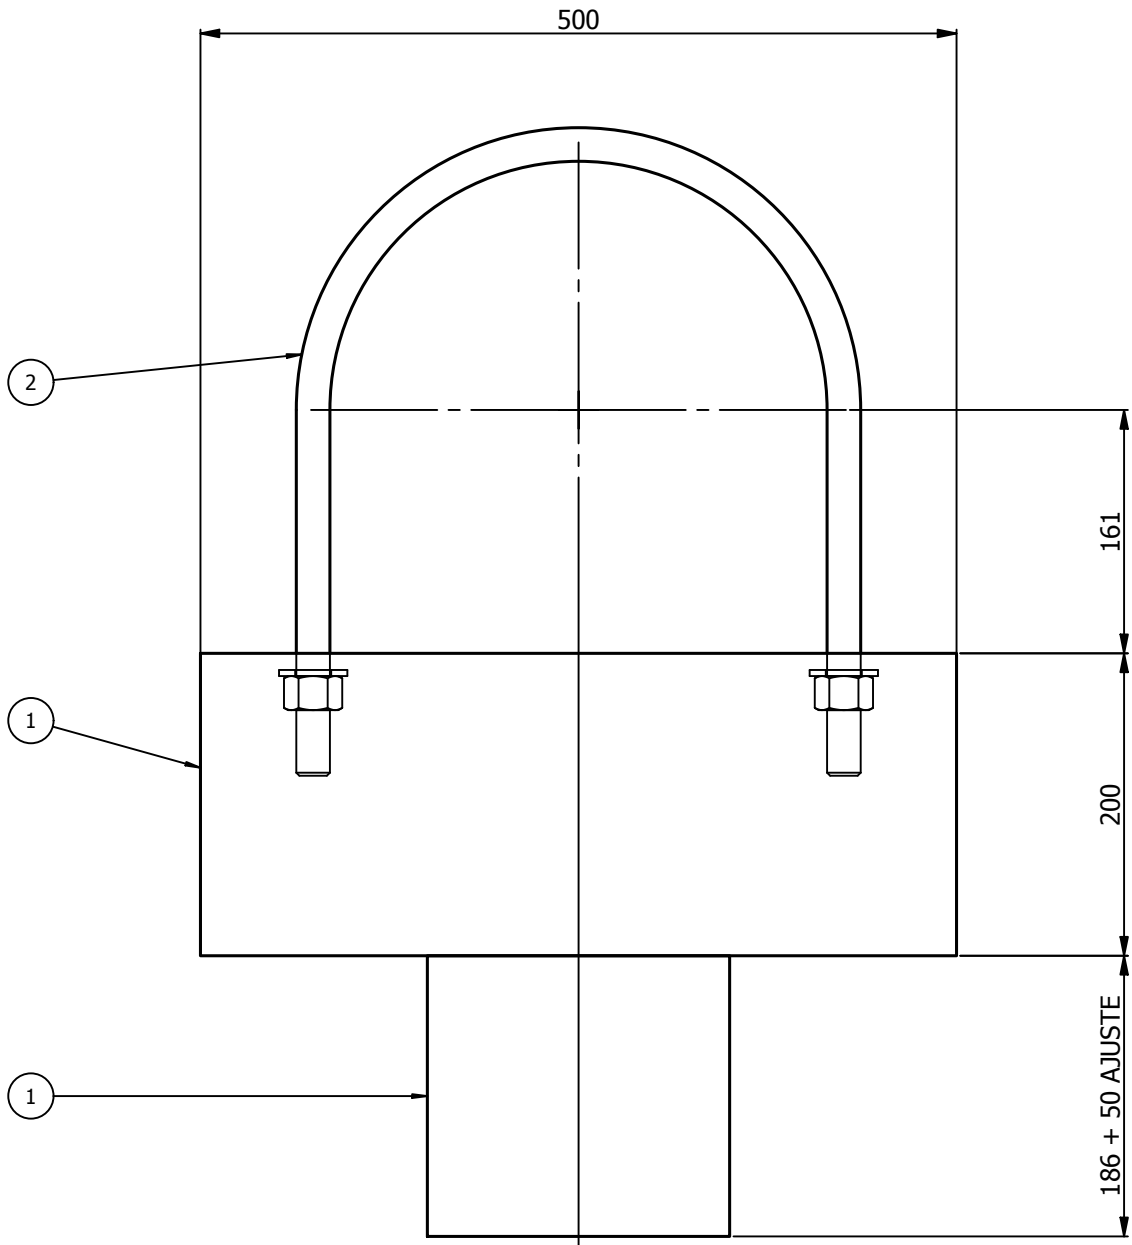

VISTA FRONTAL

ESCALA:(1:5)

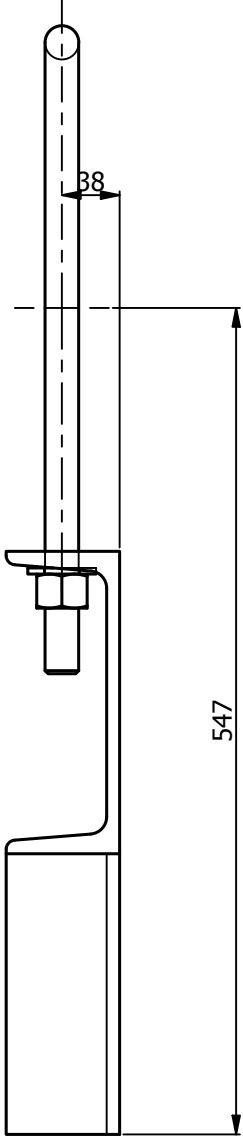

VISTA LATERAL

ESCALA:(1:5)

NOTA: LISTA DE MATERIALES PARA UNA UNIDAD


2	U-BOLT 12 C_TUERCAS Y ARAND 7_8 BRICR	1		50014795
1	PERFIL UPN 200 25.30 KG/M	0,686 m		10000194
ITEM	DESCRIPCION	CANT.	OBSERVACION	SAP

LISTA DE MATERIALES

SP-04


CANT.: 1

COLOR: Negro Ral 9011

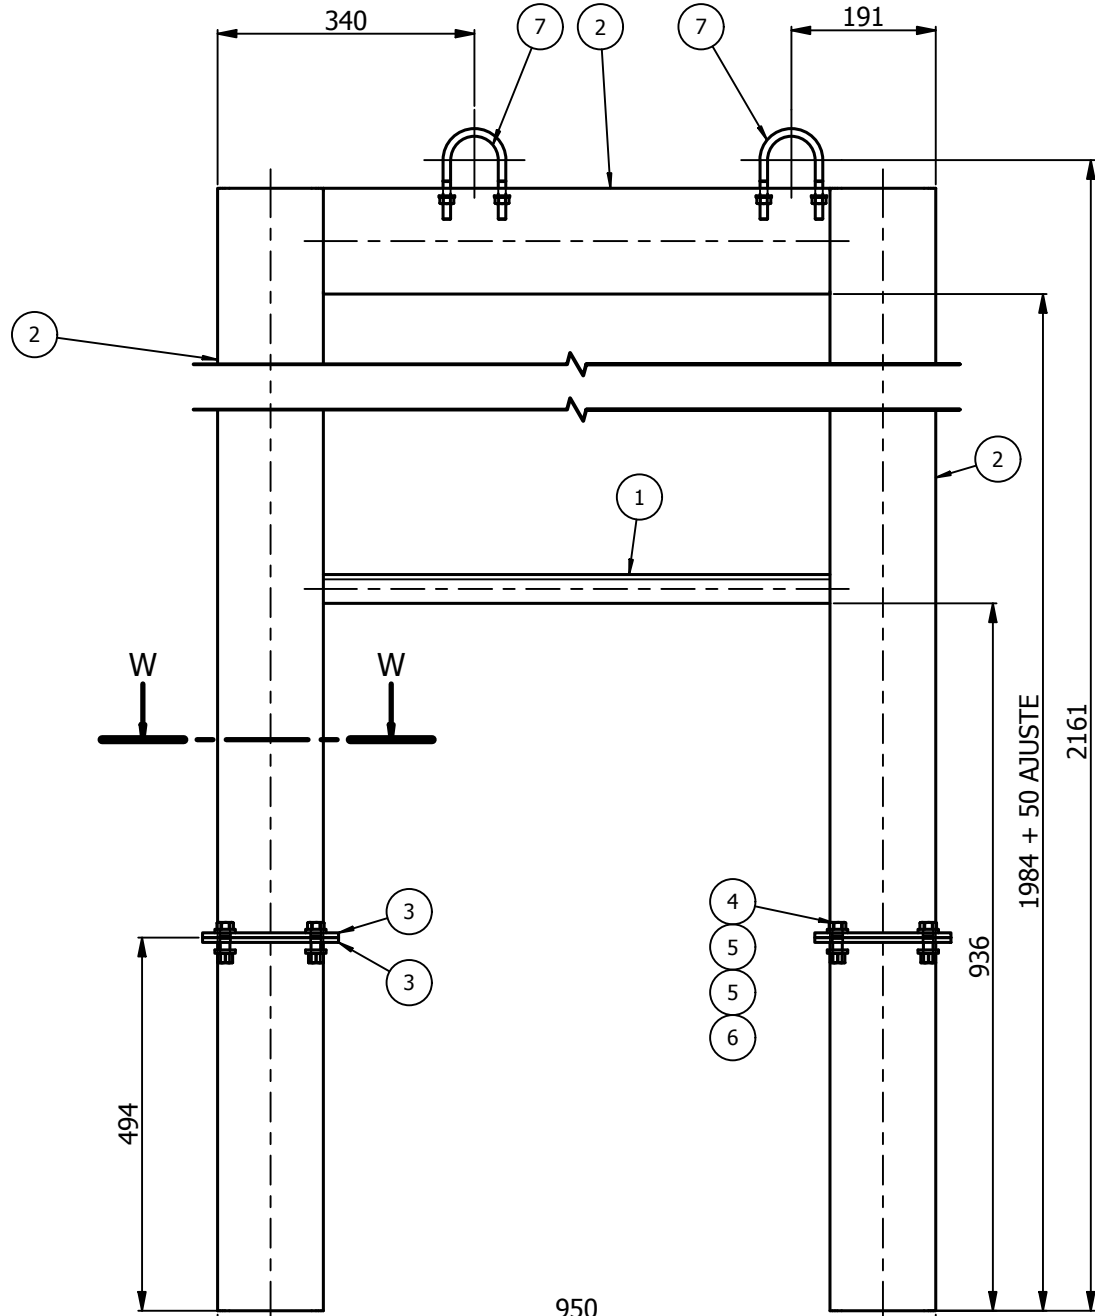


VISTA FRONTAL

ESCALA:(1 : 10)

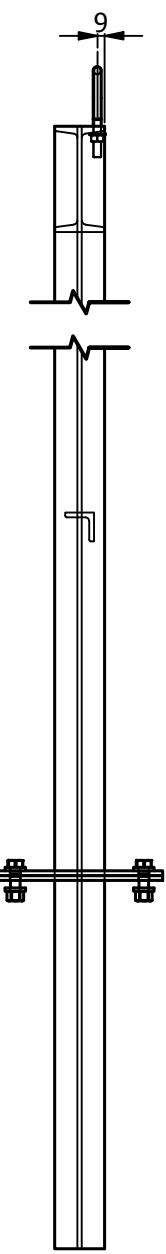

VISTA LATERAL

ESCALA:(1 : 10)

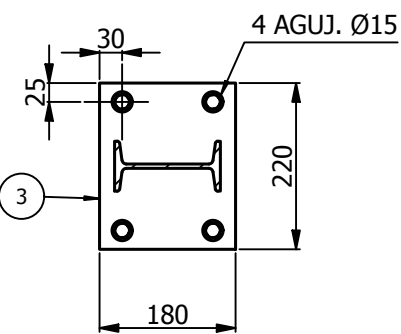

CORTE W-W

ESCALA:(1 : 10)


7	U-BOLT 2 C/TUERCAS Y ARAND ¼ BRICROM	2		50023422
6	TUERCA HEX UNC ½ DIN934 AC GALV	8		50003934
5	ARANDELA PLANA Ø½ SA-F436 BIC	16		50016372
4	BULON H UNC ½" x 1¾" DIN931 SAE-5 BICR	8		50004980
3	CHAPA ¼" IRAM F26 50,3KG/M2	0,158 m^2		10002270
2	PERFIL IPN 140 14.40KG/M	4,918 m		10000130
1	ANGULO 1½" X ¼" 3.44KG/M	0,670 m		10000042
ITEM	DESCRIPCION	CANT.	OBSERVACION	SAP

LISTA DE MATERIALES

SP-03


CANT.: 1

COLOR: Negro Ral 9011

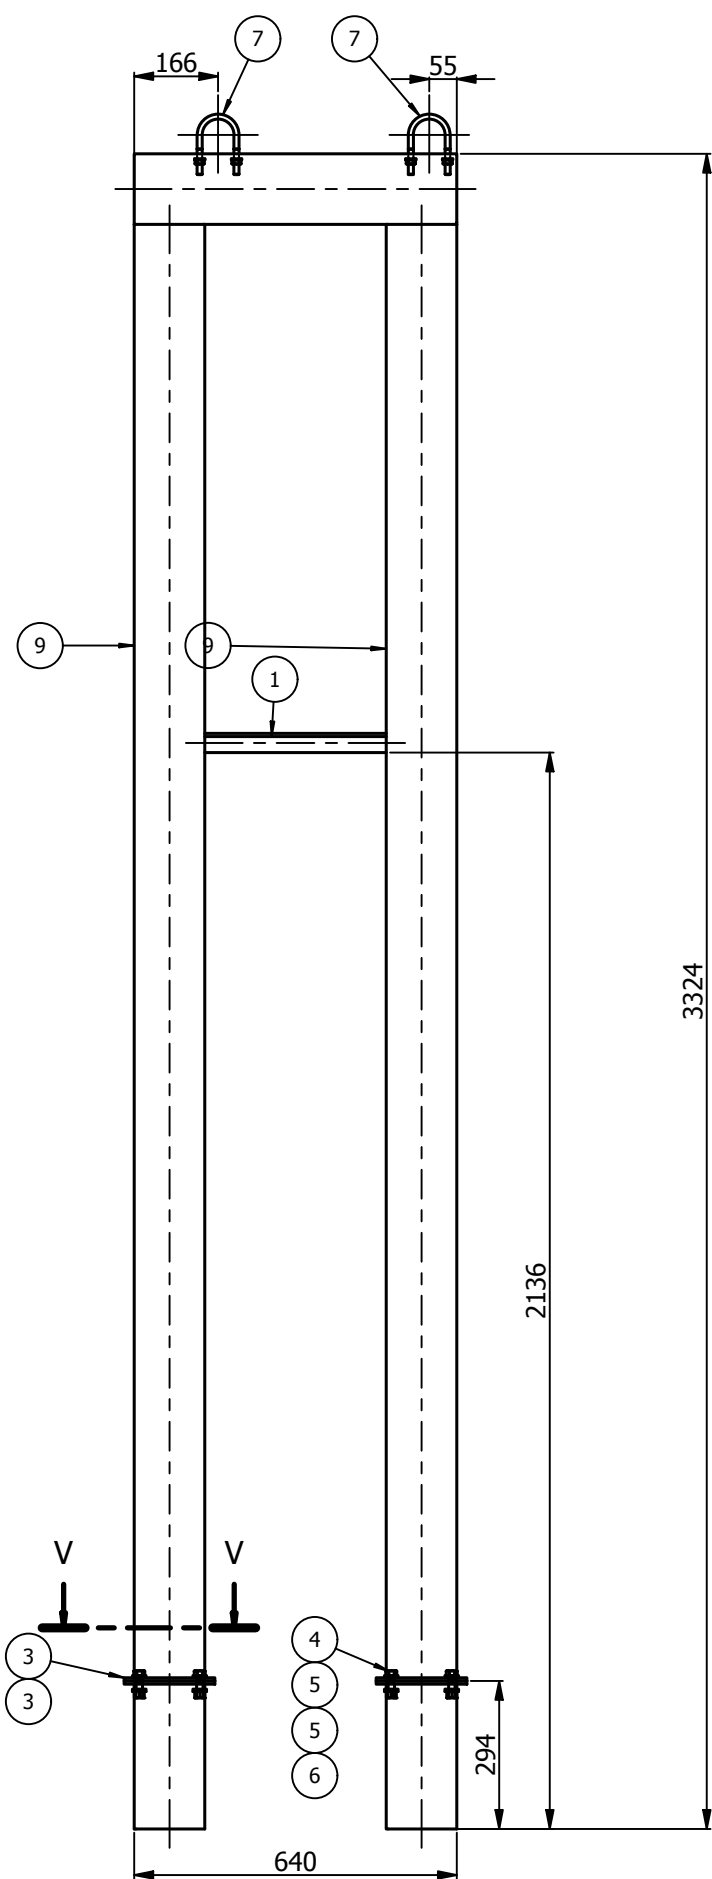

VISTA FRONTAL

ESCALA:(1:15)

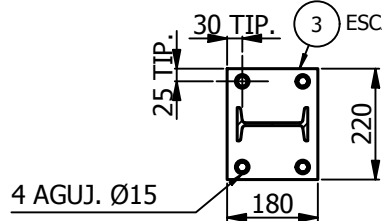


CORTE V-V

ESCALA:(1:15)

9	PERFIL IPN 140 14.40KG/M	6,368 m		10000130
8	PERFIL IPN 140 14.40KG/M	0,640 m		10000130
7	U-BOLT 2 C/TUERCAS Y ARAND ¼ BRICROM	2		50023422
6	TUERCA HEX UNC ½ DIN934 AC GALV	8		50003934
5	ARANDELA PLANA Ø½ SA-F436 BIC	16		50016372
4	BULON H UNC ½" x 1¾" DIN931 SAE-5 BICR	8		50004980
3	CHAPA ¼" IRAM F26 50,3KG/M2	0,158 m^2		10002270
1	ANGULO 1½" X ¼" 3.44KG/M	0,360 m		10000042
ITEM	DESCRIPCION	CANT.	OBSERVACION	SAP

LISTA DE MATERIALES

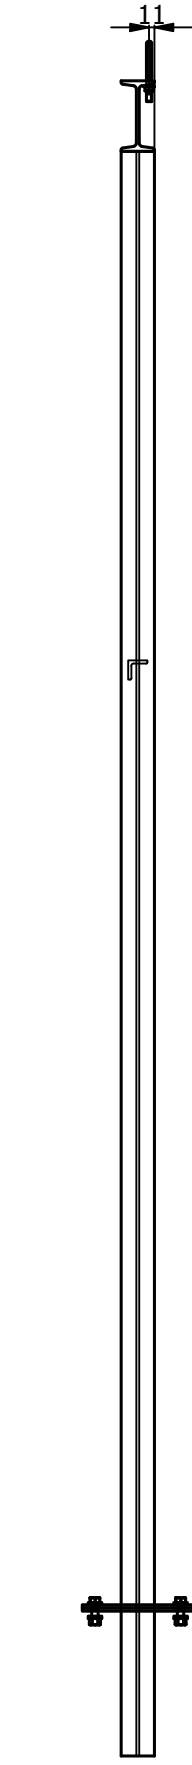


VISTA LATERAL

ESCALA:(1:15)

SP-05


CANT.: 1

COLOR: Negro Ral 9011

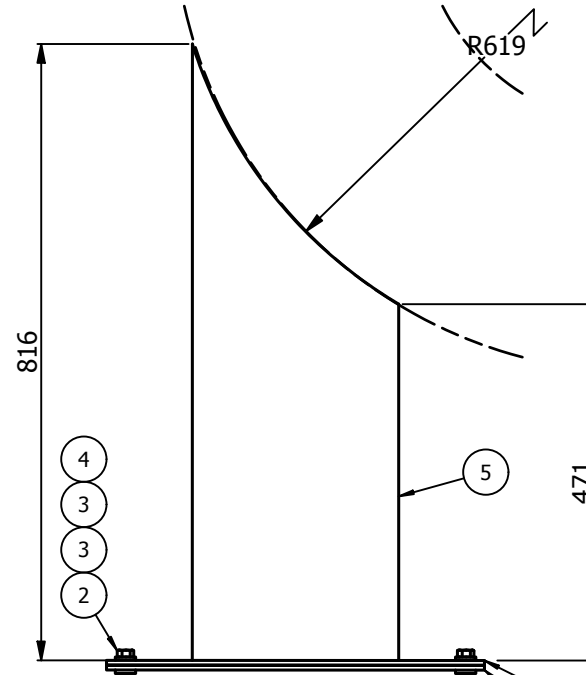


VISTA FRONTAL

ESCALA:(1 : 10)

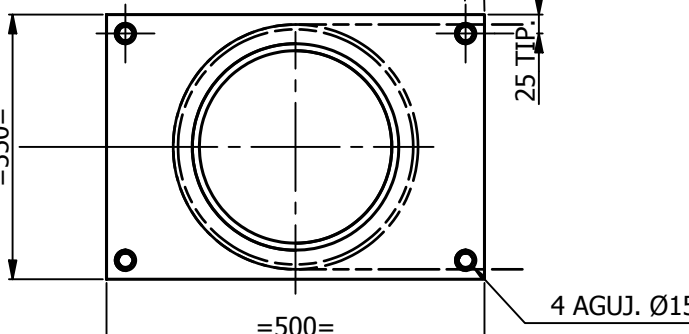

VISTA EN PLANTA

ESCALA:(1 : 10)

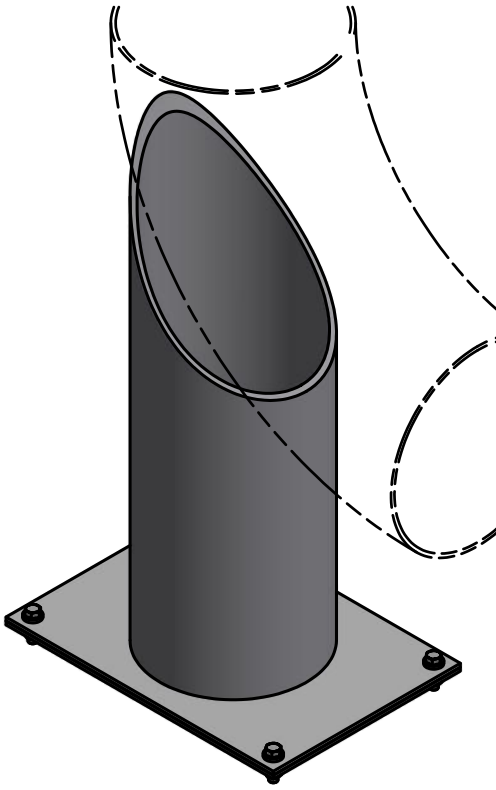

VISTA ISOMETRICA

ESCALA:(1 : 10)

NOTA: LISTA DE MATERIALES PARA UNA UNIDAD


5	CAÑO S/C NPS 10 SCH40 SA 106 GR B	0,83 m		10001411
4	TUERCA HEX UNC ½ DIN934 AC GALV	4		50003934
3	ARANDELA PLANA Ø½ SA-F436 BIC	8		50016372
2	BULON H UNC ½" x 1¾" DIN931 SAE-5 BICR	4		50004980
1	CHAPA ¼" IRAM F26 50,3KG/M2	0,350 m^2		10002270
ITEM	DESCRIPCION	CANT.	OBSERVACION	SAP

LISTA DE MATERIALES

SP-06


CANT.: 16

COLOR: Negro Ral 9011

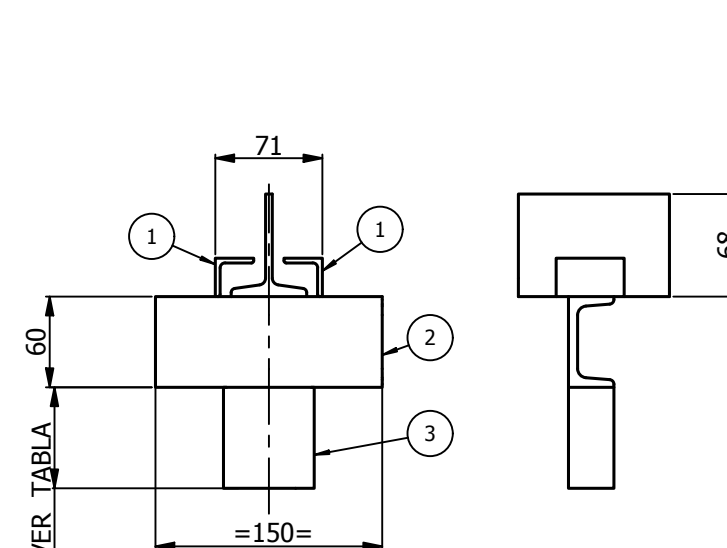

VISTA FRONTAL

ESCALA:(1 : 5)

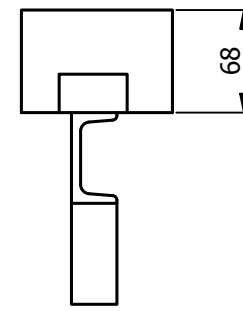


VISTA LATERAL

ESCALA:(1 : 5)

F	17	7
E	30	4
D	42	1
C	50	1
B	58	1
A	65	2
NOMENCLATURA	LONGITUD	CANTIDAD
SOPORTE		

PATIN SOLDADO A CAÑERÍA (REFERENCIA)

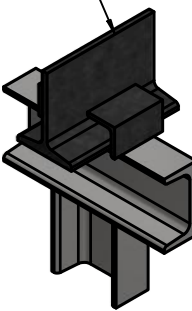

VISTA ISOMETRICA

ESCALA:(1 : 5)

NOTA: LISTA DE MATERIALES PARA UNA UNIDAD

3	PERFIL UPN 65 7.09 KG/M	0,067 m		10001713
2	PERFIL UPN 65 7.09 KG/M	0,150 m		10001713
1	ANGULO 1" x 1/8" 1.21Kg/m	0,090 m		10000027
ITEM	DESCRIPCION	CANT.	OBSERVACION	SAP

LISTA DE MATERIALES

- 1) CORTAR SOPORTES MAS LARGOS PARA AJUSTAR c/ CAÑERÍAS. APROX 50mm.
- 2) SOLDAR SOPORTES A SKID.
- 3) LA UBICACION Y DIMENSIONES DE LOS SOPORTES SON DE REFERENCIA Y DEBERA AJUSTARSE DURANTE EL MONTAJE C/EL PIPING.
- 4) TODAS LAS DIMENSIONES ESTAN INDICADAS EN mm, SALVO INDICACION CONTRARIA.